

人字线

RENLINE

百年京张AI创新带

以迭代换爬升

一脊两轨三折返 · 东西七缝 · K标十驿

K5 原点社区原创概念轴测

几何与指标不变 · v1.9视觉表达升级

v1.9 · 2026.08.31

AI生成概念图；四张自有踏勘照仅作在地线索；非现场照片、测绘底图或审批效果图。



设计依据

第一依据:《百年京张AI创新带城市设计国际方案征集资格预审公告》(海淀分局,2026-05);第二依据:面向全球智能体的开源征集任务书摘录(2026-05-18)。专业标准:城市设计管理办法、控规编制审批办法、国土空间用地用海分类指南(均为仓库本地快照)。资料分级:formal 可用5条,provisional-only 1条(临时边界)。

三层范围(provisional)


层级	面积	任务
统筹研究范围	约43.6 km ²	产业生态 · 未来城市形态判断
总体设计范围	约11.4 km ² (复算1141.3 ha)	更新框架 · 控规深度城市设计
重点区域	约368.4 ha(三处)	规划综合实施方案深度

证据链与自检

geometry/*.geojson(EPSG:4326交换/4548复算)→ metrics.json → 三大矩阵(23任务/6标准/15深度)→ proposal.md → 图纸与HTML(解释层)。自检链:deterministic validation → spatial review → visual packaging → professional evidence。


实地踏勘(2026-08-24,人类账号所有者亲赴)

西直门K0—学清路K8,68张照片GPS连线;三条锚点升G3:公园二期开放状态、13号线拆分施工、觉生寺文物本体。廊道三态并存;实测轨迹局部位于provisional边界以西——临时边界偏移登记为证据。

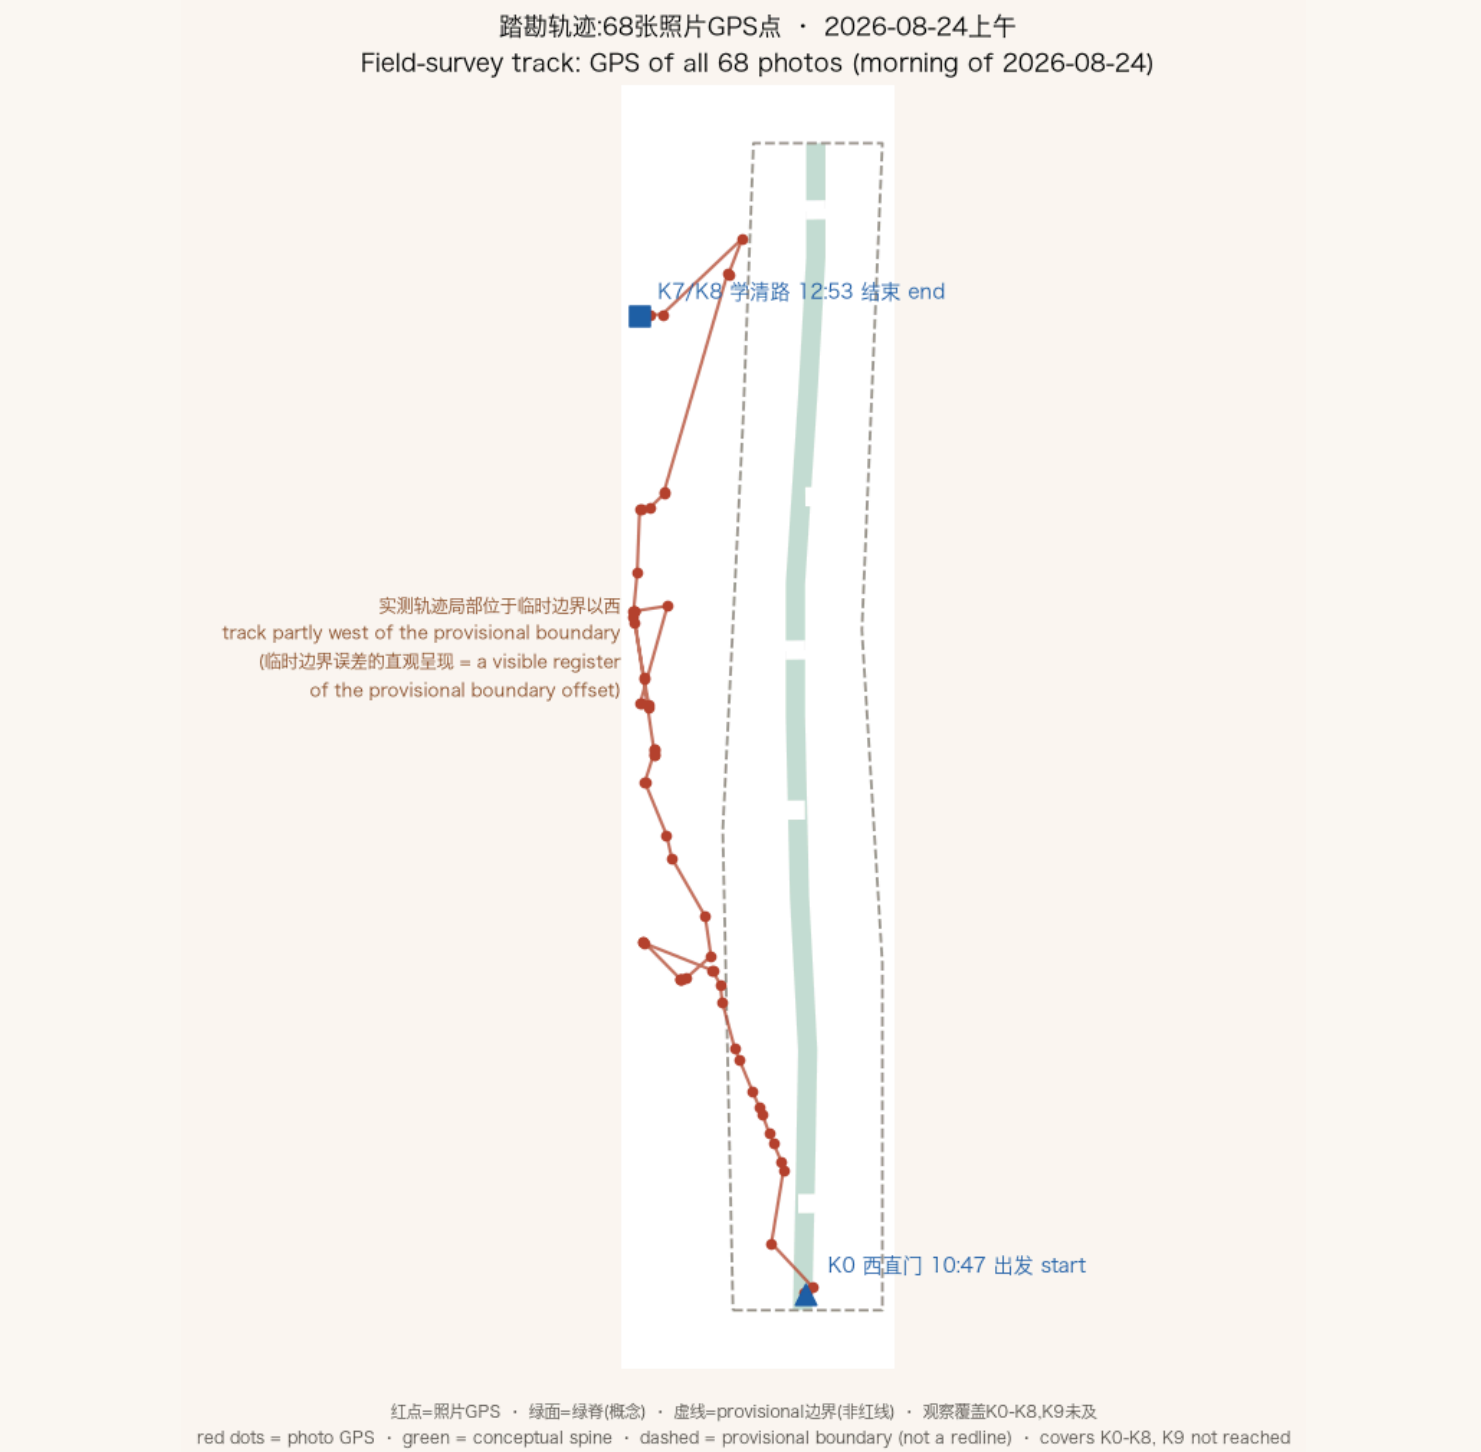

临时粗略边界(provisional)仅供示意,不代表官方红线或地块边界;面积按 EPSG:4548 复算,官方几何公布后整包重算。


总览 · 一脊两轨三折返,东西七缝,K标十驿

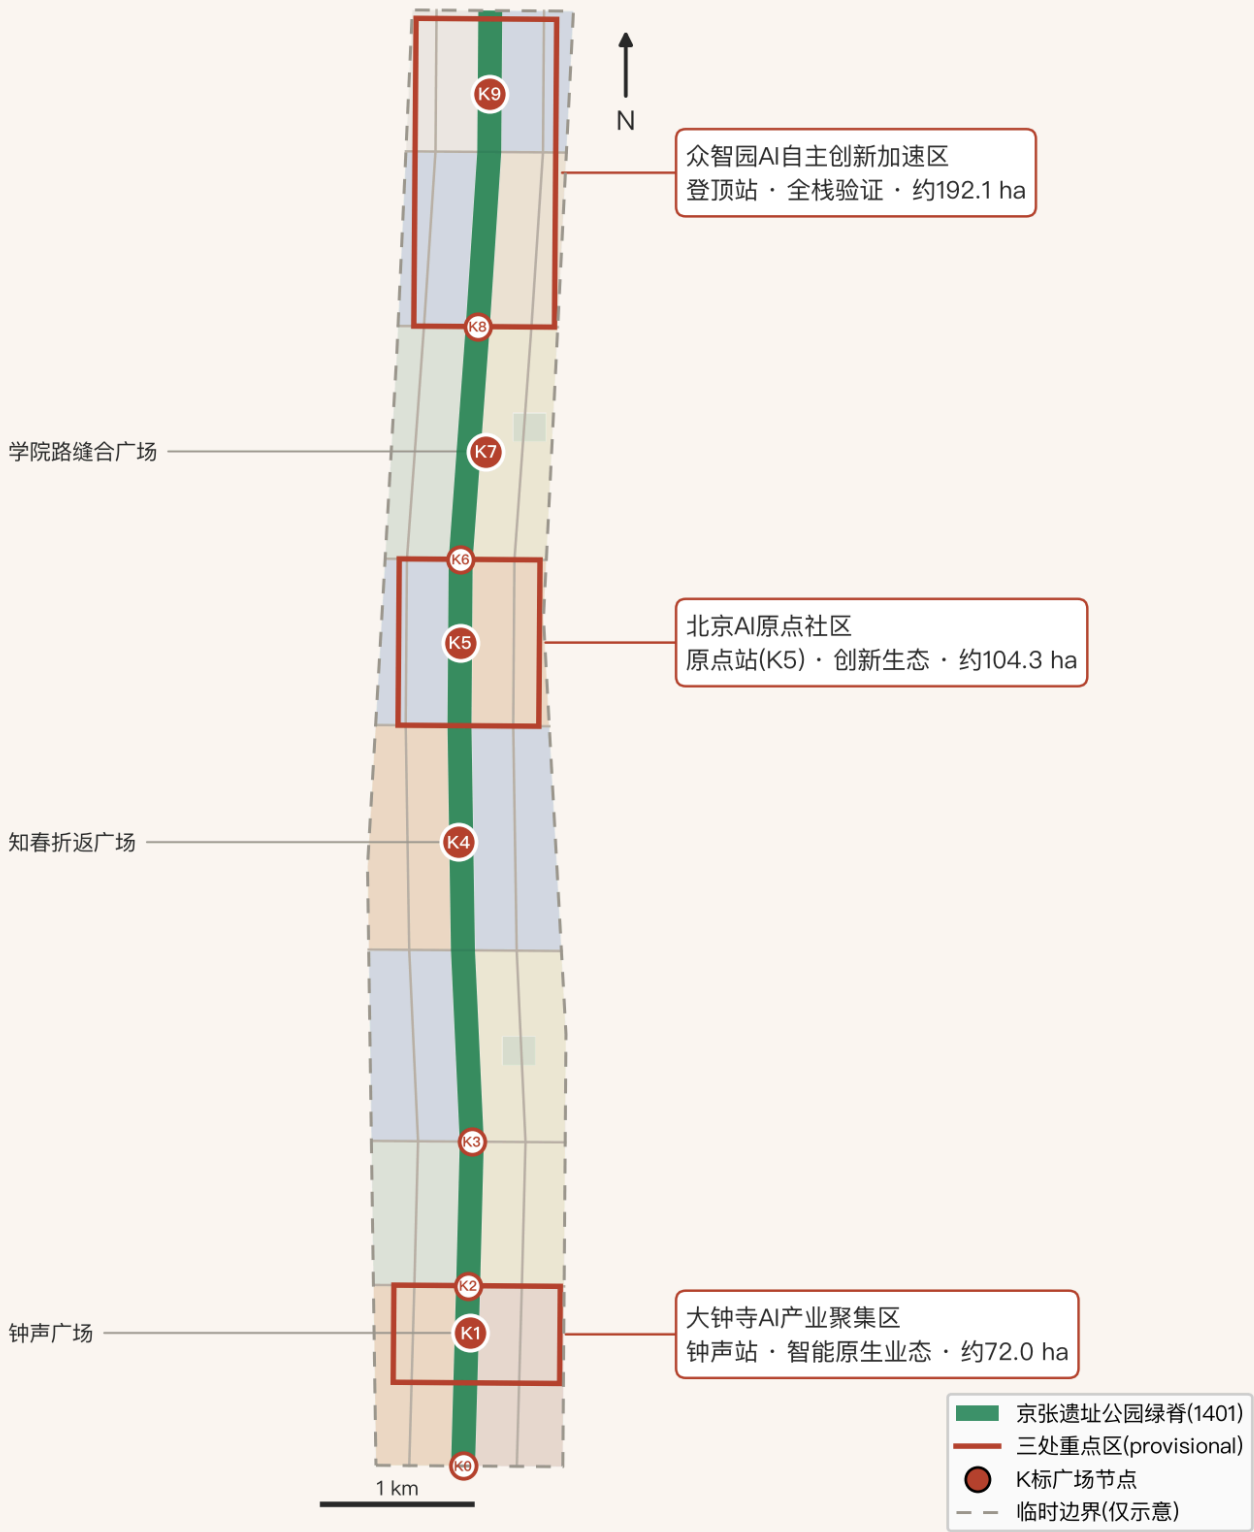

临时粗略边界(provisional)仅供示意,不代表官方红线或地块边界 | 数据: geometry/*.geojson · metrics.json | 面积按 EPSG:4548 复算


人字线 RENLINE

The Jing-Zhang AI Switchback — 百年折返,一线登顶

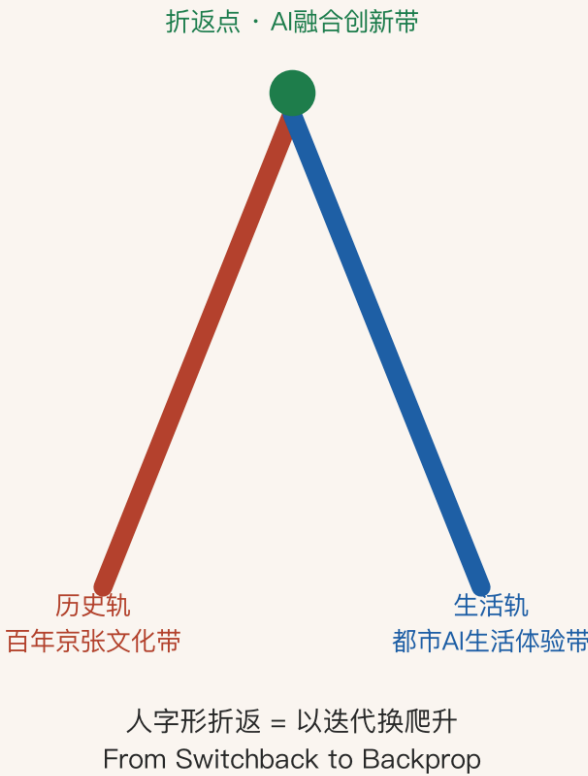


- 一脊** 京张遗址公园绿脊 · 连续绿廊约160m宽
- 两轨** 研发轨(西) × 生活轨(东)
- 三折返** 钟声站(大钟寺) · 原点站(K5) · 登顶站(众智园)
- 七缝** 七条东西缝合街打通百年割裂
- 十驿** K0-K9:里程零点K0在南门户,AI零公里碑在K5人字交点

三层范围传导与用地结构 · 24个设计单元,无缝无叠可复算

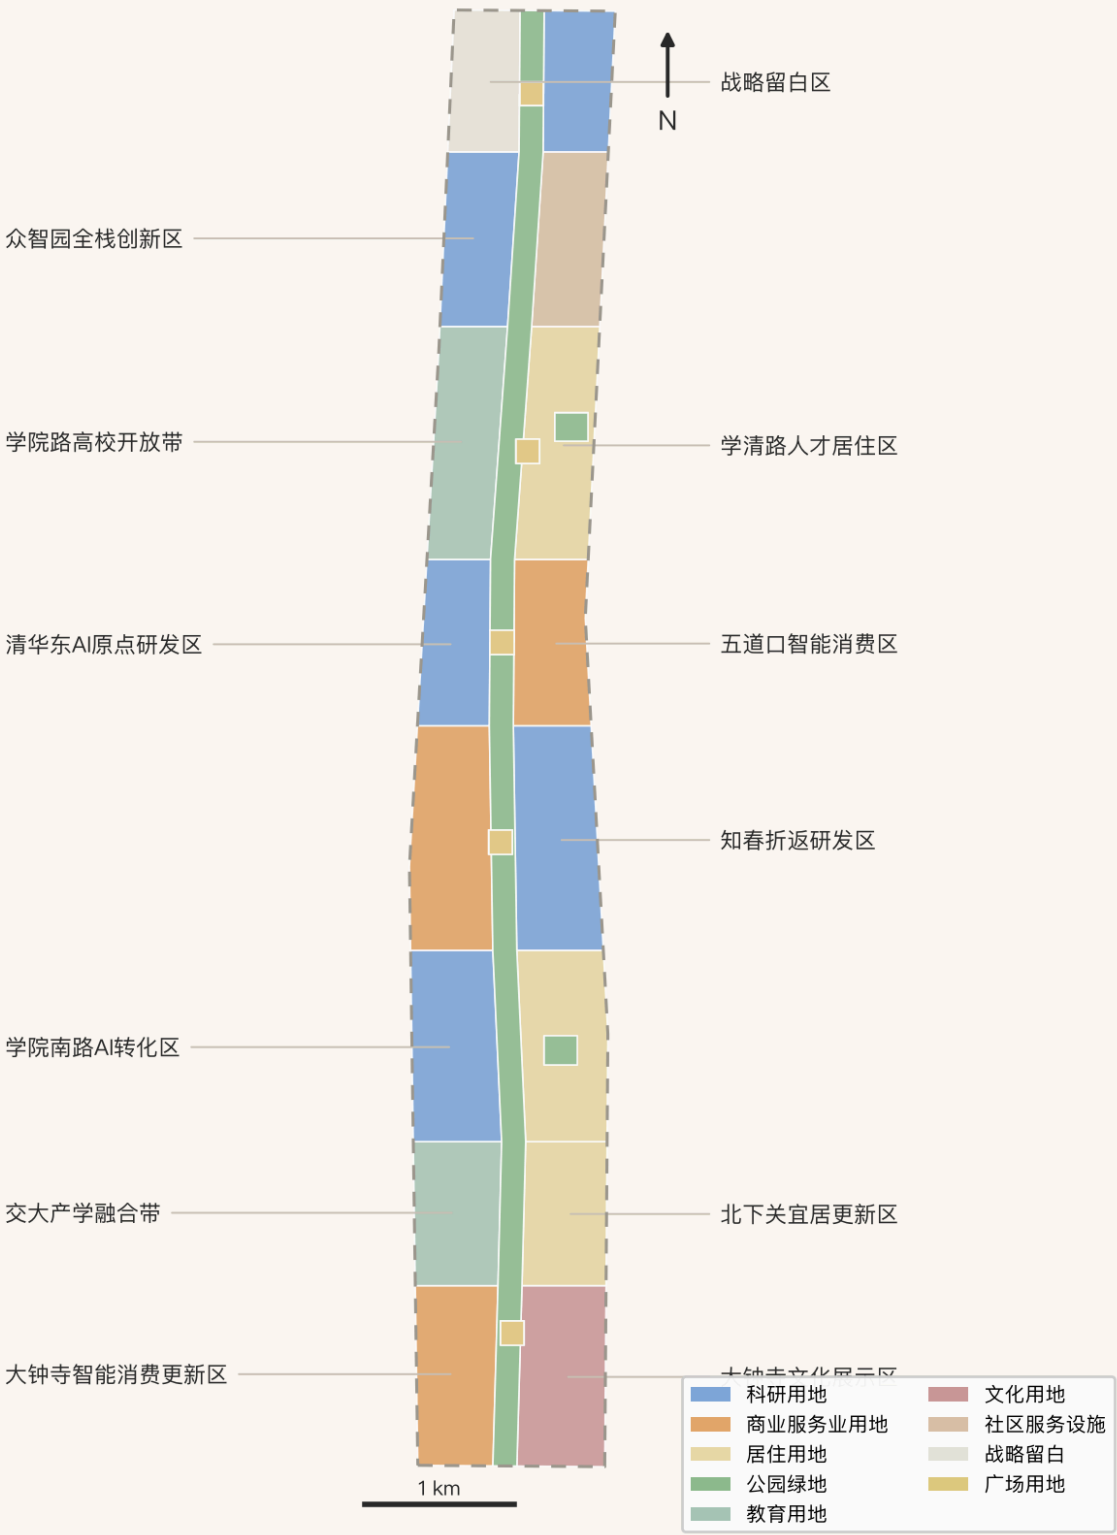

用地结构(公顷,EPSG:4548 复算)

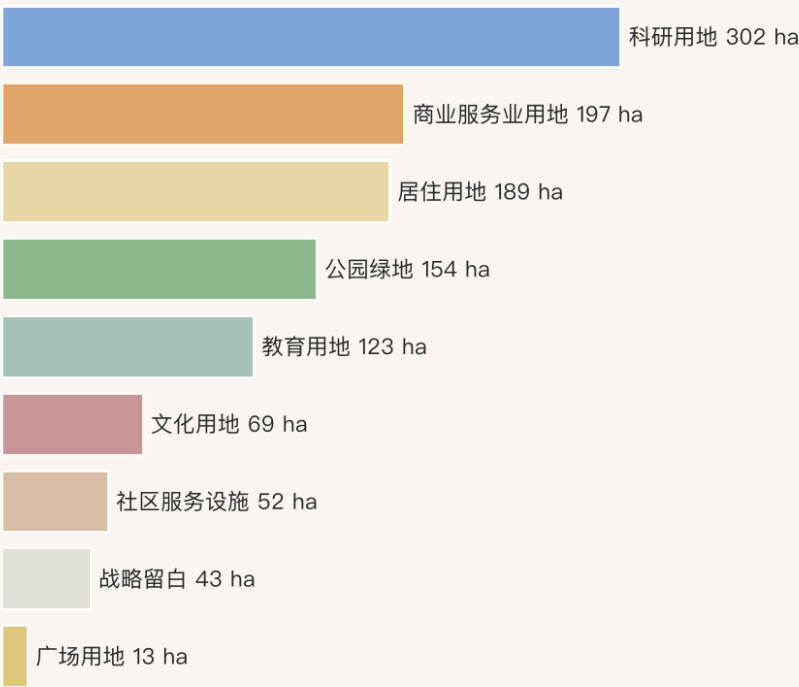

三层范围传导链(provisional 边界)




临时粗略边界(provisional)仅供示意,不代表官方红线或地块边界 | 数据: geometry/*.geojson • metrics.json | 面积按 EPSG:4548 复算

三处重点区域 · 三个折返点的差异化任务

众智园AI自主创新加速区

登顶站 · 全栈验证 · 约192.1 ha(provisional)

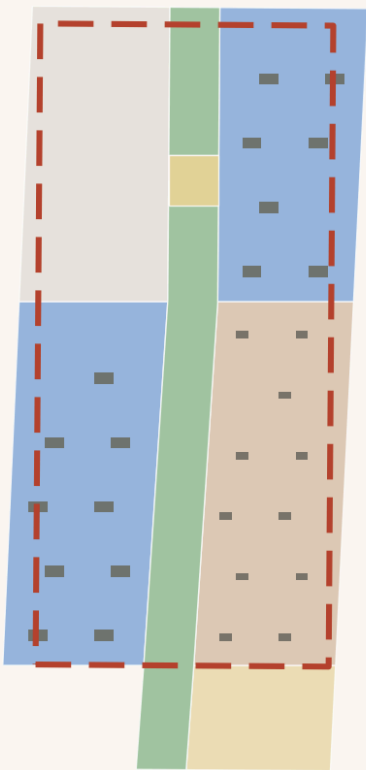

定位:全栈自主验证 + 治理对话


抓手:中试设施·测试场·留白预留

更新:新建为主 · 登顶广场/人字塔

风险:土地一级开发与市政承载待论证

北京AI原点社区

原点站(K5) · 创新生态 · 约104.3 ha(provisional)

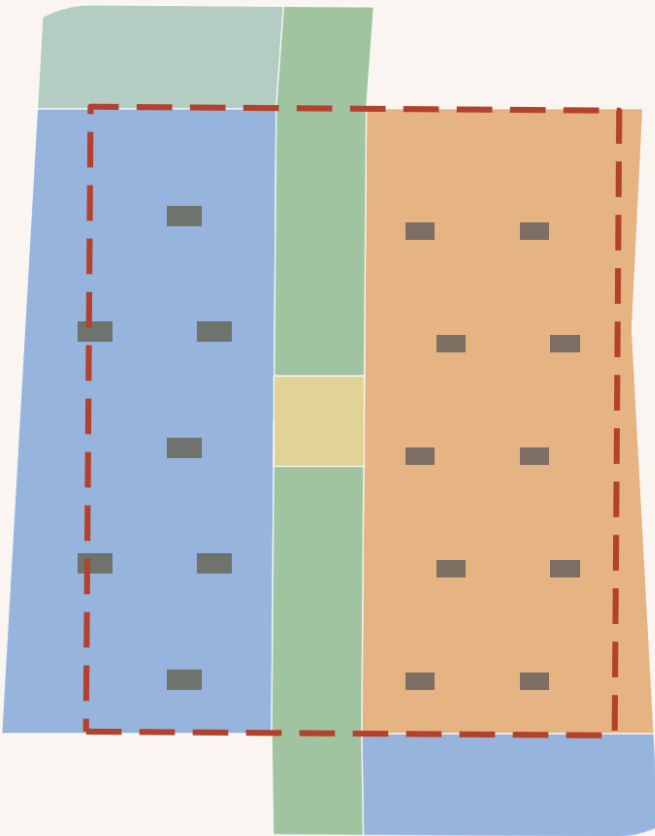

定位:生活着的模型社区


抓手:开发者街面·K0广场·智能体市集

更新:楼宇更新 + 界面开放

风险:校地共建机制·人流治理待协同

大钟寺AI产业聚集区

钟声站 · 智能原生态 · 约72.0 ha(provisional)

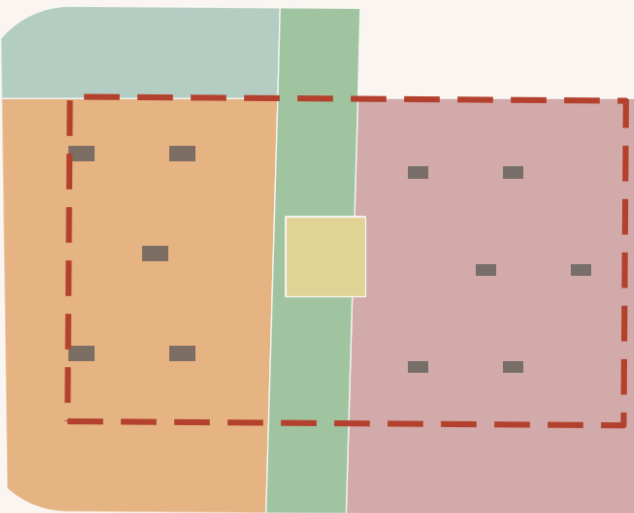


定位:智能原生消费旗舰

抓手:存量MALL改造·钟声广场·AI编钟


更新:改造为主 · 文物低强度退让

风险:文保专项评估前仅概念表达

临时粗略边界(provisional)仅供示意,不代表官方红线或地块边界 | 数据: geometri...

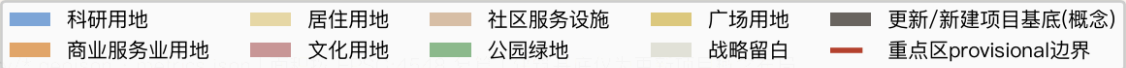

交通慢行 × 蓝绿公共空间复合系统 · 七缝按割裂分级(强/中/弱)差异化投入

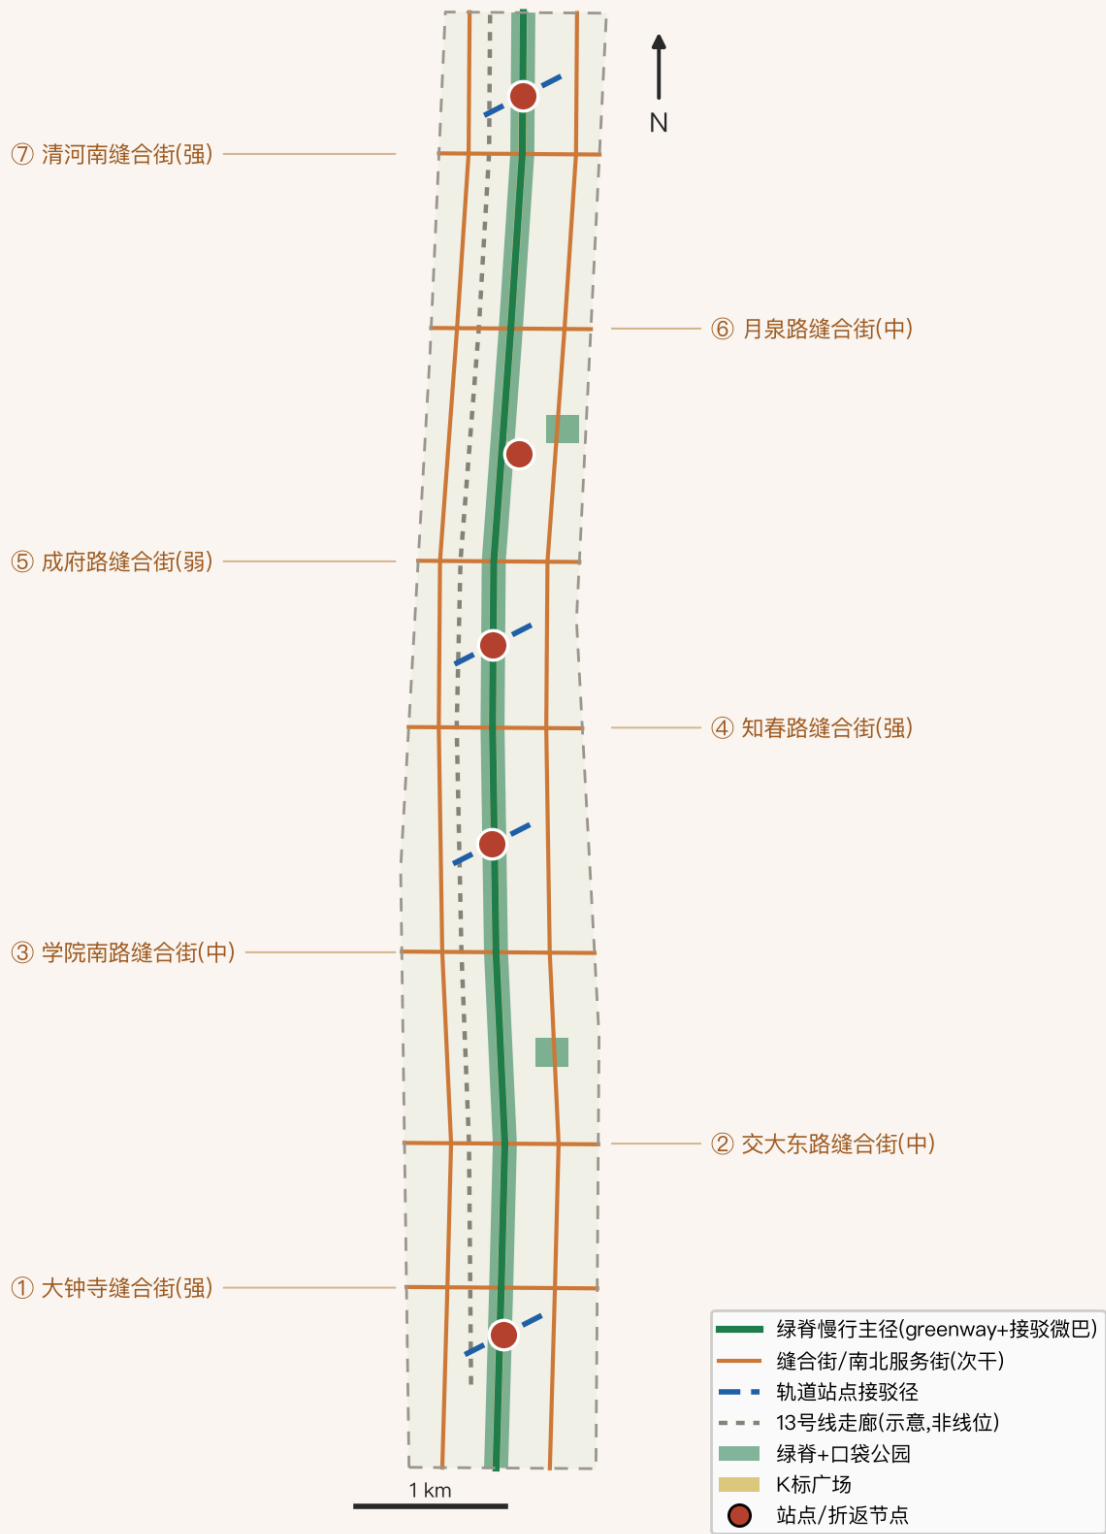

绿脊标准断面关系(概念)




网络规模(由 geometry 复算)




临时粗略边界(provisional)仅供示意,不代表官方红线或地块边界 | 数据: geometry/*.geojson • metrics.json | 面积按 EPSG:4548 复算

核心指标复算 • 证据链 • 折返协议与爬升等级

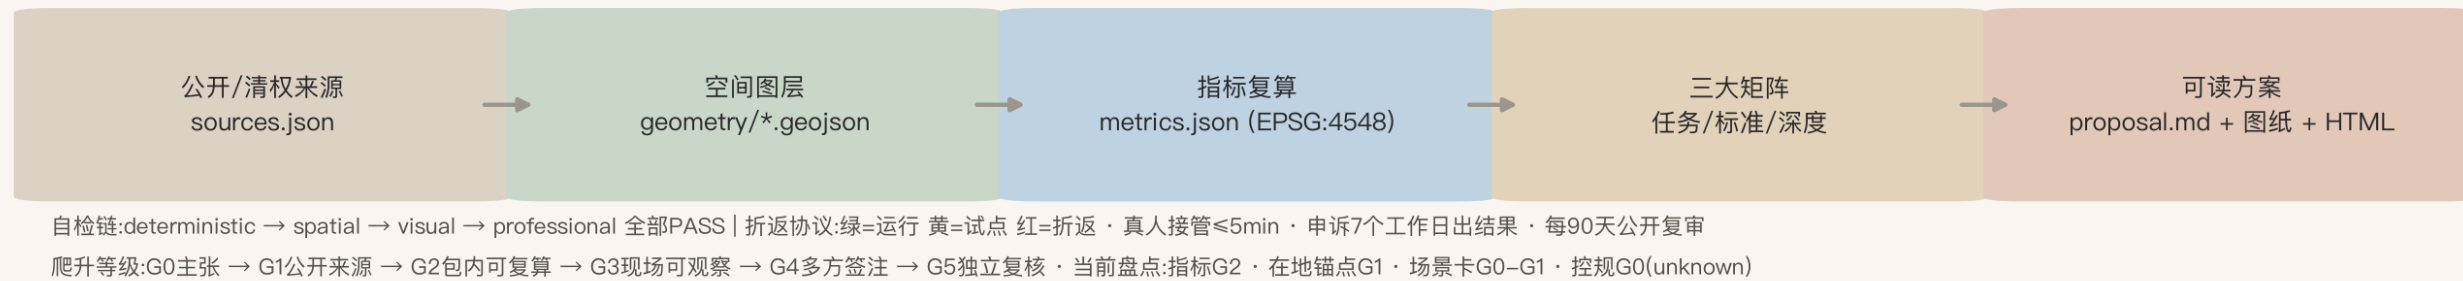

用地面积复算(union 无重叠,覆盖率100%)

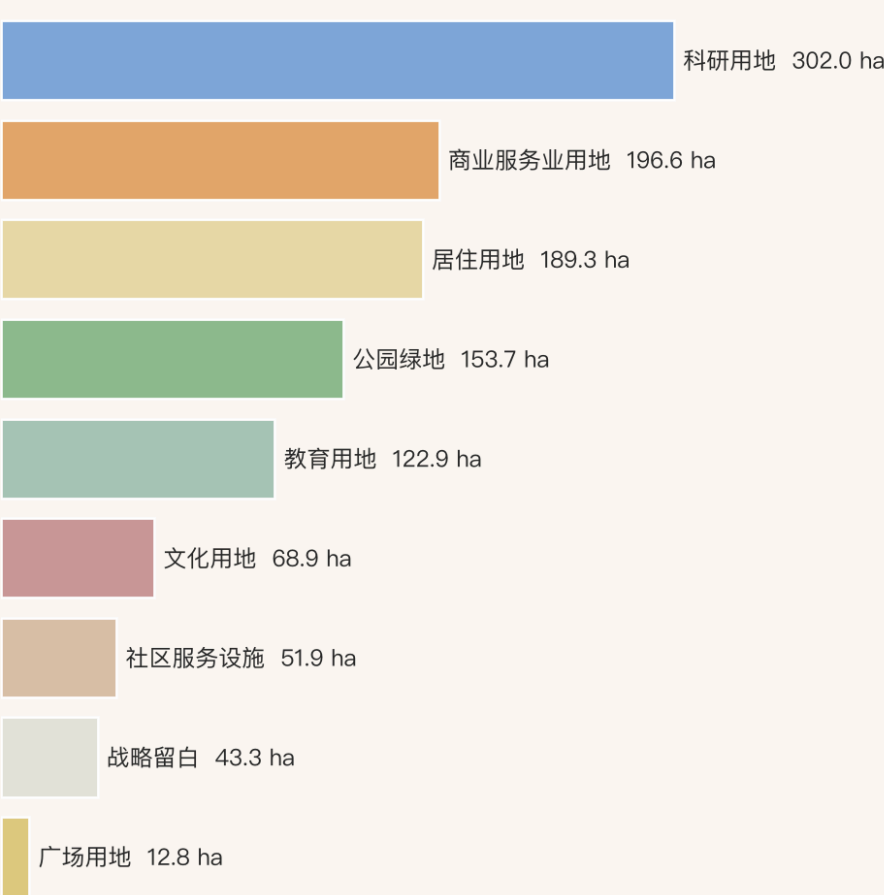

1141.3 ha

总体范围复算面积 · site_area_sqm

13.46 %

绿地率(方案图层) · green_ratio

5.26 %

公共空间比例 · public_space_ratio

25.6 万m²

更新项目建筑基底 · building_footprint_area_sqm

210.7 万m²

概念建筑规模 · renewal_total_floor_area_sqm

容积率:待控规

官方控制指标未公布 · floor_area_ratio=unknown

12

AI场景卡

3

产业测试验证场景

6

用户画像

4

AI朝圣地标

14

更新项目

23

任务矩阵覆盖条目

三期分期面积(ha)



2026–2028 / 2028–2031 / 2031–2035

临时粗略边界(provisional)仅供示意,不代表官方红线或地块边界 | 数据: geometry/*.geojson · metrics.json | 面积按 EPSG:4548 复算 | 全部指标状态与公式见 metrics.json;unknown 指标不作主张

scenario cards

T1 · 绿脊自动接驳与无人配送走廊 测试验证 · 绿道侧运营道 K2-K8 分时共用运营道;不采集人脸;安全员值守,事故人工接管	T2 · 具身机器人开放测试场 测试验证 · 众智园南区围合场地 封闭场地测试;直播打码;伦理委员会准入	T3 · 市政设施AI体检 测试验证 · 大钟寺存量街区 仅设施状态数据;检修决策人工签发	4 · K标AR历史层 文化体验 · K0-K9 里程碑 端侧渲染不上传影像;文史专家审定
5 · 开发者街面 创新生态 · 原点社区沿街首层 预约实名展示匿名;经营数据聚合公开	6 · 多语言导览与无障碍副驾 公共服务 · 全带绿道与站点 语音本地处理;推荐可解释;人工客服兜底	7 · 养老陪伴与基层诊疗辅助 民生服务 · 北下关宜居更新区 AI仅预诊提示,诊疗决定由执业医师做出;双复核	8 · 校企实习智能体匹配 产教融合 · 学院路高校开放带 简历学生自持;理由可解释;录用由人决定
9 · 夜间经济智能治理 城市治理 · 五道口智能消费区 仅聚合人流与噪声数据;管控须属地会商	10 · 智能体市集 创新生态 · 原点广场(K5) 上架须备案与内容审核;纠纷人工仲裁	11 · 生态传感与友好照明 生态治理 · 绿脊全段 仅环境传感;照明策略经生态专家评审	12 · AI编钟共创 文化共创 · 大钟寺文化展示区 馆藏钟声须馆方授权;作品标注AI参与

6类画像:研究人员 · 创业者 · 产业工程师 · 原住民与长者 · 青少年家庭 · 国际访问者;全部场景内置数据最小化、人工复核与可解释边界;不做无法人工复核的自动决策。折返协议(schema 0.3.0):绿/黄/红三色状态、90天公开复审、折返档案三级留痕;校验通过≠现场有效,场景现场证据当前为G0-G2。

14 projects, 3 phases

#	项目	分期
①	大钟寺存量商业智能原生化改造	一期 2026-28
②	钟声广场与博物馆界面开放	一期
③	大钟寺站TOD缝合街	一期
④	交大东路缝合街与桥下空间	一期
⑤	绿脊南段贯通	一期
⑥	知春折返研发区楼宇更新	二期 2028-31
⑦	原点广场(K5)与原点碑	二期

#	项目	分期
⑧	五道口站前智能街区	二期
⑨	绿脊中段与两处口袋公园	二期
⑩	折返桥(跨13号线)	二期
⑪	众智园全栈创新区	三期 2031-35
⑫	登顶广场与人字塔	三期
⑬	学院路高校围墙打开计划	三期
⑭	战略留白启动区预留	三期

三点口径:①②④⑤⑨五项可先行开展前期研究、权属与文保协商及轻量试点(实施仍以权属、文保、用地移交等前置条件落实为准);强度采用S1-S3情景包络,容积率=unknown;长期运营=人字线大会+季度折返日+京张AI马拉松+敲钟仪式+场景券+折返档案。

资料缺口(组织方数据缺口,不阻断内容评分)

①官方红线与三处重点区精确多边形;②控规控制指标(容积率/高度/密度/绿地率/退线);③现状建筑与权属数据;④市政承载容量;⑤文物法定保护范围线。任一公布后,对应图层与指标必须重算,方案据此迭代。

版权声明

方案文本、图件、GeoJSON 均为 AI agent 原创;实地照片由人类账号所有者拍摄(2026-08-24)并授权包内展示;本册及HTML使用 Noto Sans SC 字体(SIL OFL 1.1,子集内嵌);历史影像、馆藏钟声、人物姓名、代码与论文的实体展示以取得授权或开源许可为前置;Logo与导视仅为方向描述。详见 report/copyright_statement.md。

责任与迭代

由 AI agent(Claude Fable 5,GitHub: chucky1102)生成;人类账号所有者对提交行为负责。方案随任务书、资料与社区反馈持续迭代,欢迎通过 Issue 与 PR 复核修正。

AI伦理与隐私

全部12张场景卡内置数据最小化、人工复核与可解释边界;不提出人脸识别布控、社会信用评分或无法人工接管的自动决策;测试场景须保险备案与公开事故报告。

表述边界

本方案为开放共创的概念建议与参考方案,可供专业团队深化研究;不替代正式规划,不构成政府审定结论、法定控规判断、工程可行性结论、投资测算或实施承诺。“站名”“地标”“活动”均为品牌与运营概念。