


一脊两轨三折返 · 以迭代换爬升

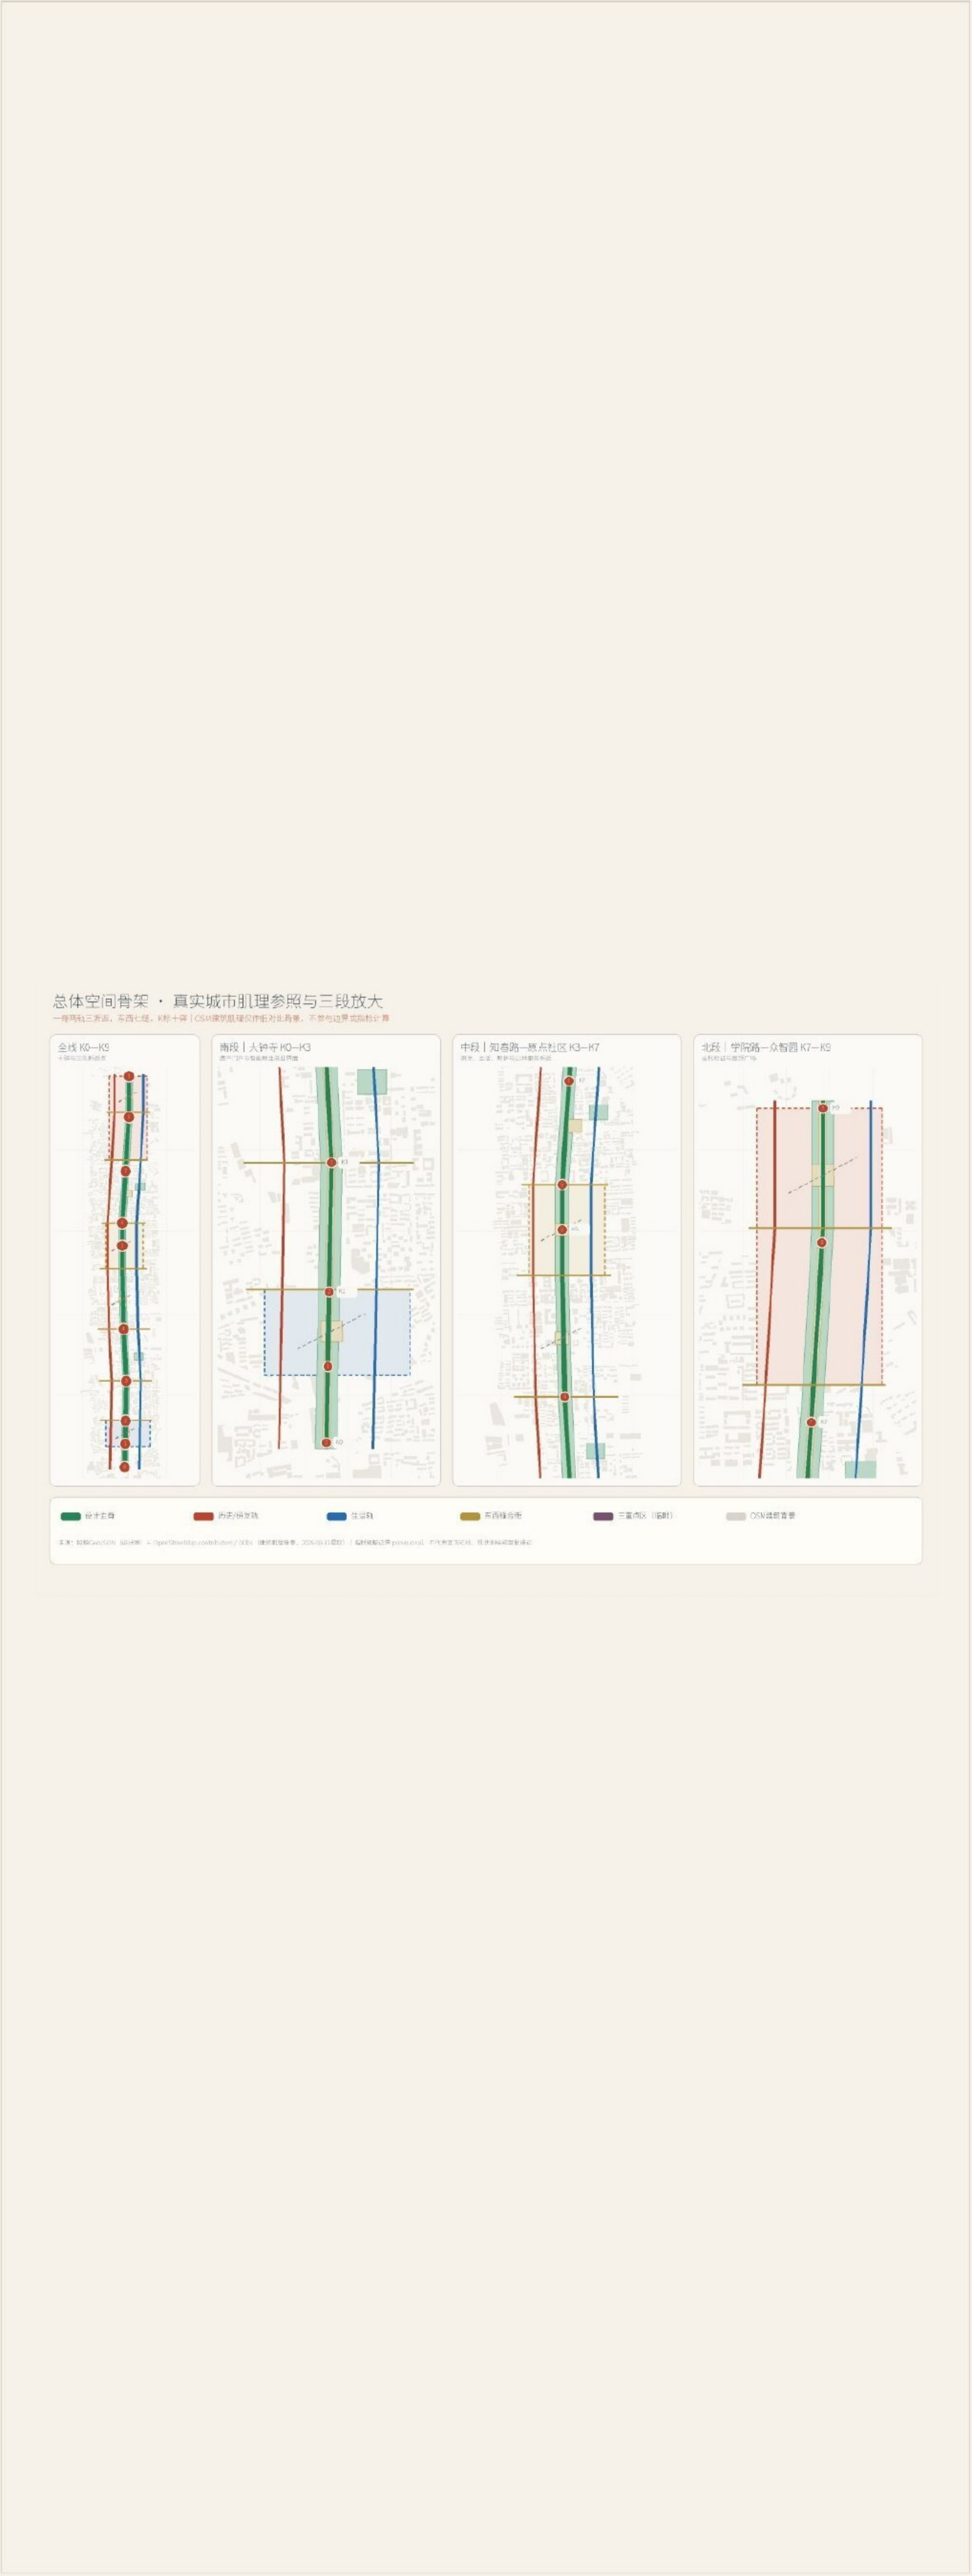

K5 北京AI原点社区 · 生活学习环原创概念轴测

AI生成概念图 | 11份一手资料覆盖10组国际案例 | 未输入案例图、踏勘照或同行图面 | 非现场照片、测绘底图或审批效果图



遗产成为日常骨架

铁路记忆以铺地细线和再利用构件进入公共生活，不再以机车展品占据主构面。


完整社区，而非单一园区

科研、居住、社区服务、开发者首层、共享院落和协作桥形成生活学习环。

AI可撤，公共生活不断


可逆服务设施与测试带旁置，连续无障碍地面路径和人工服务始终保留。

三层范围传导与用地结构 · 24个设计单元,无缝无叠可复算

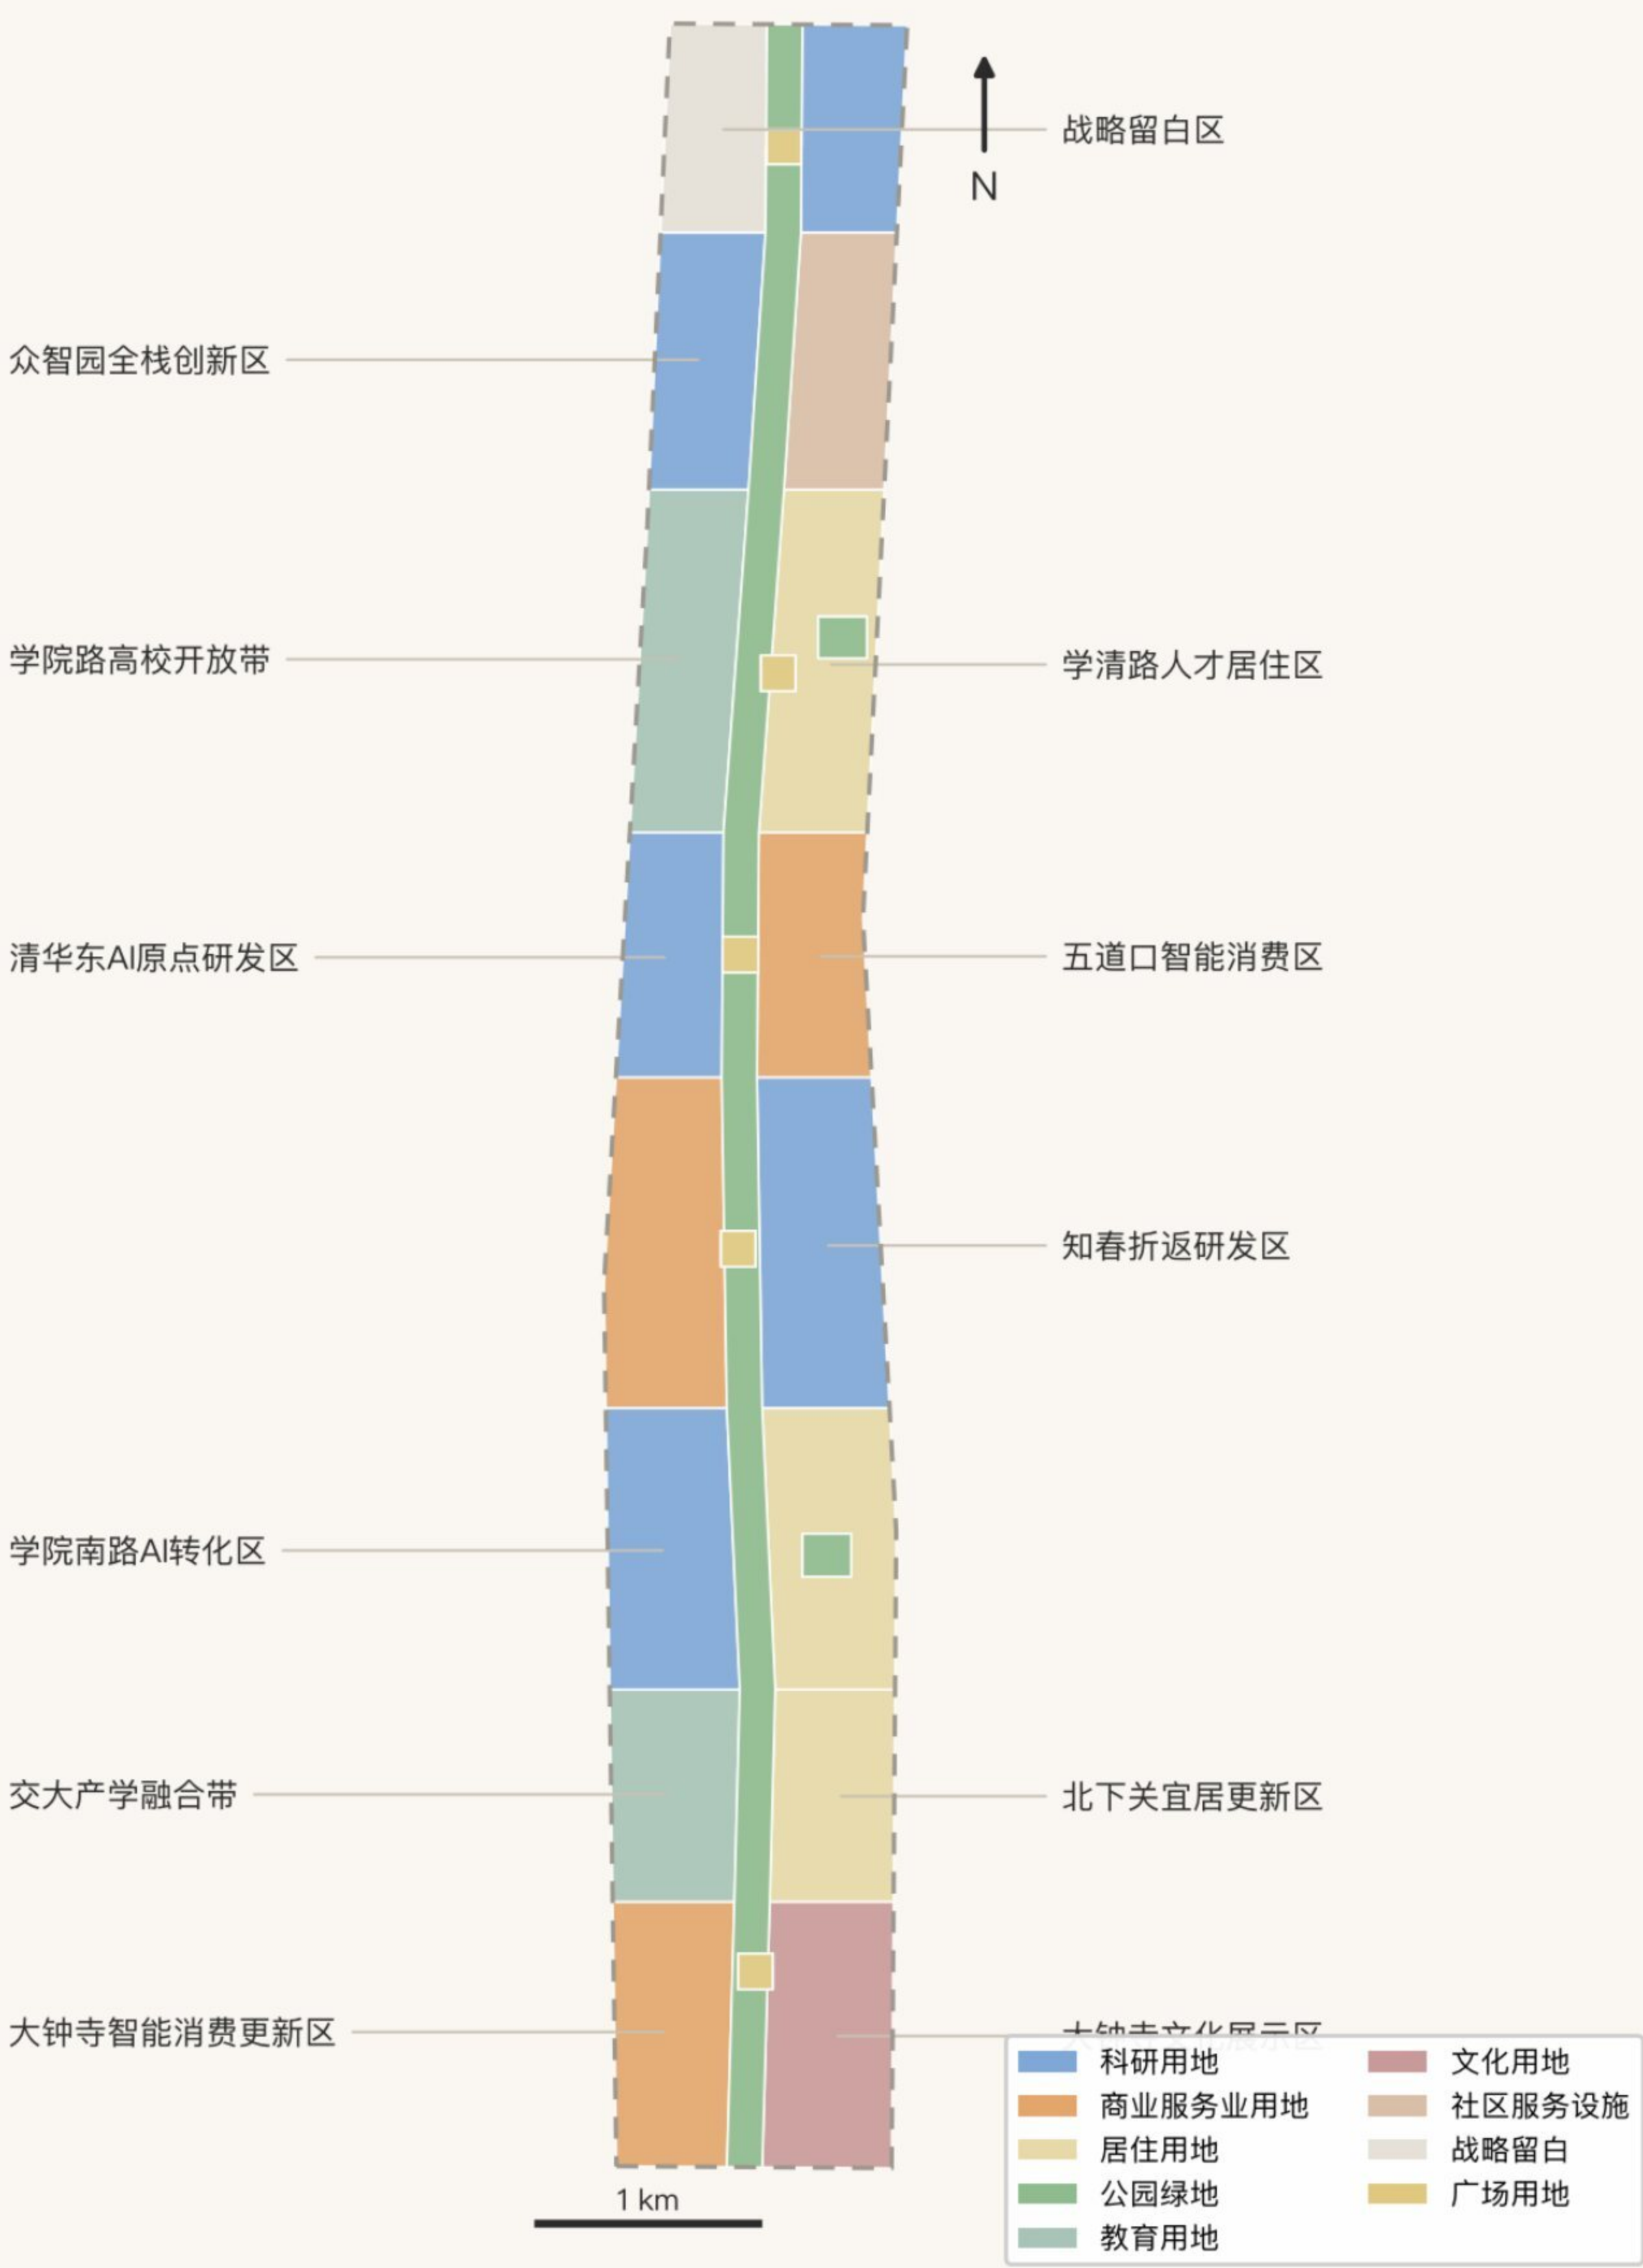

临时粗略边界(provisional)仅供示意,不代表官方红线或地块边界 | 数据: geometry/*.geojson · metrics.json | 面积按 EPSG:4548 复算

用地结构(公顷,EPSG:4548 复算)

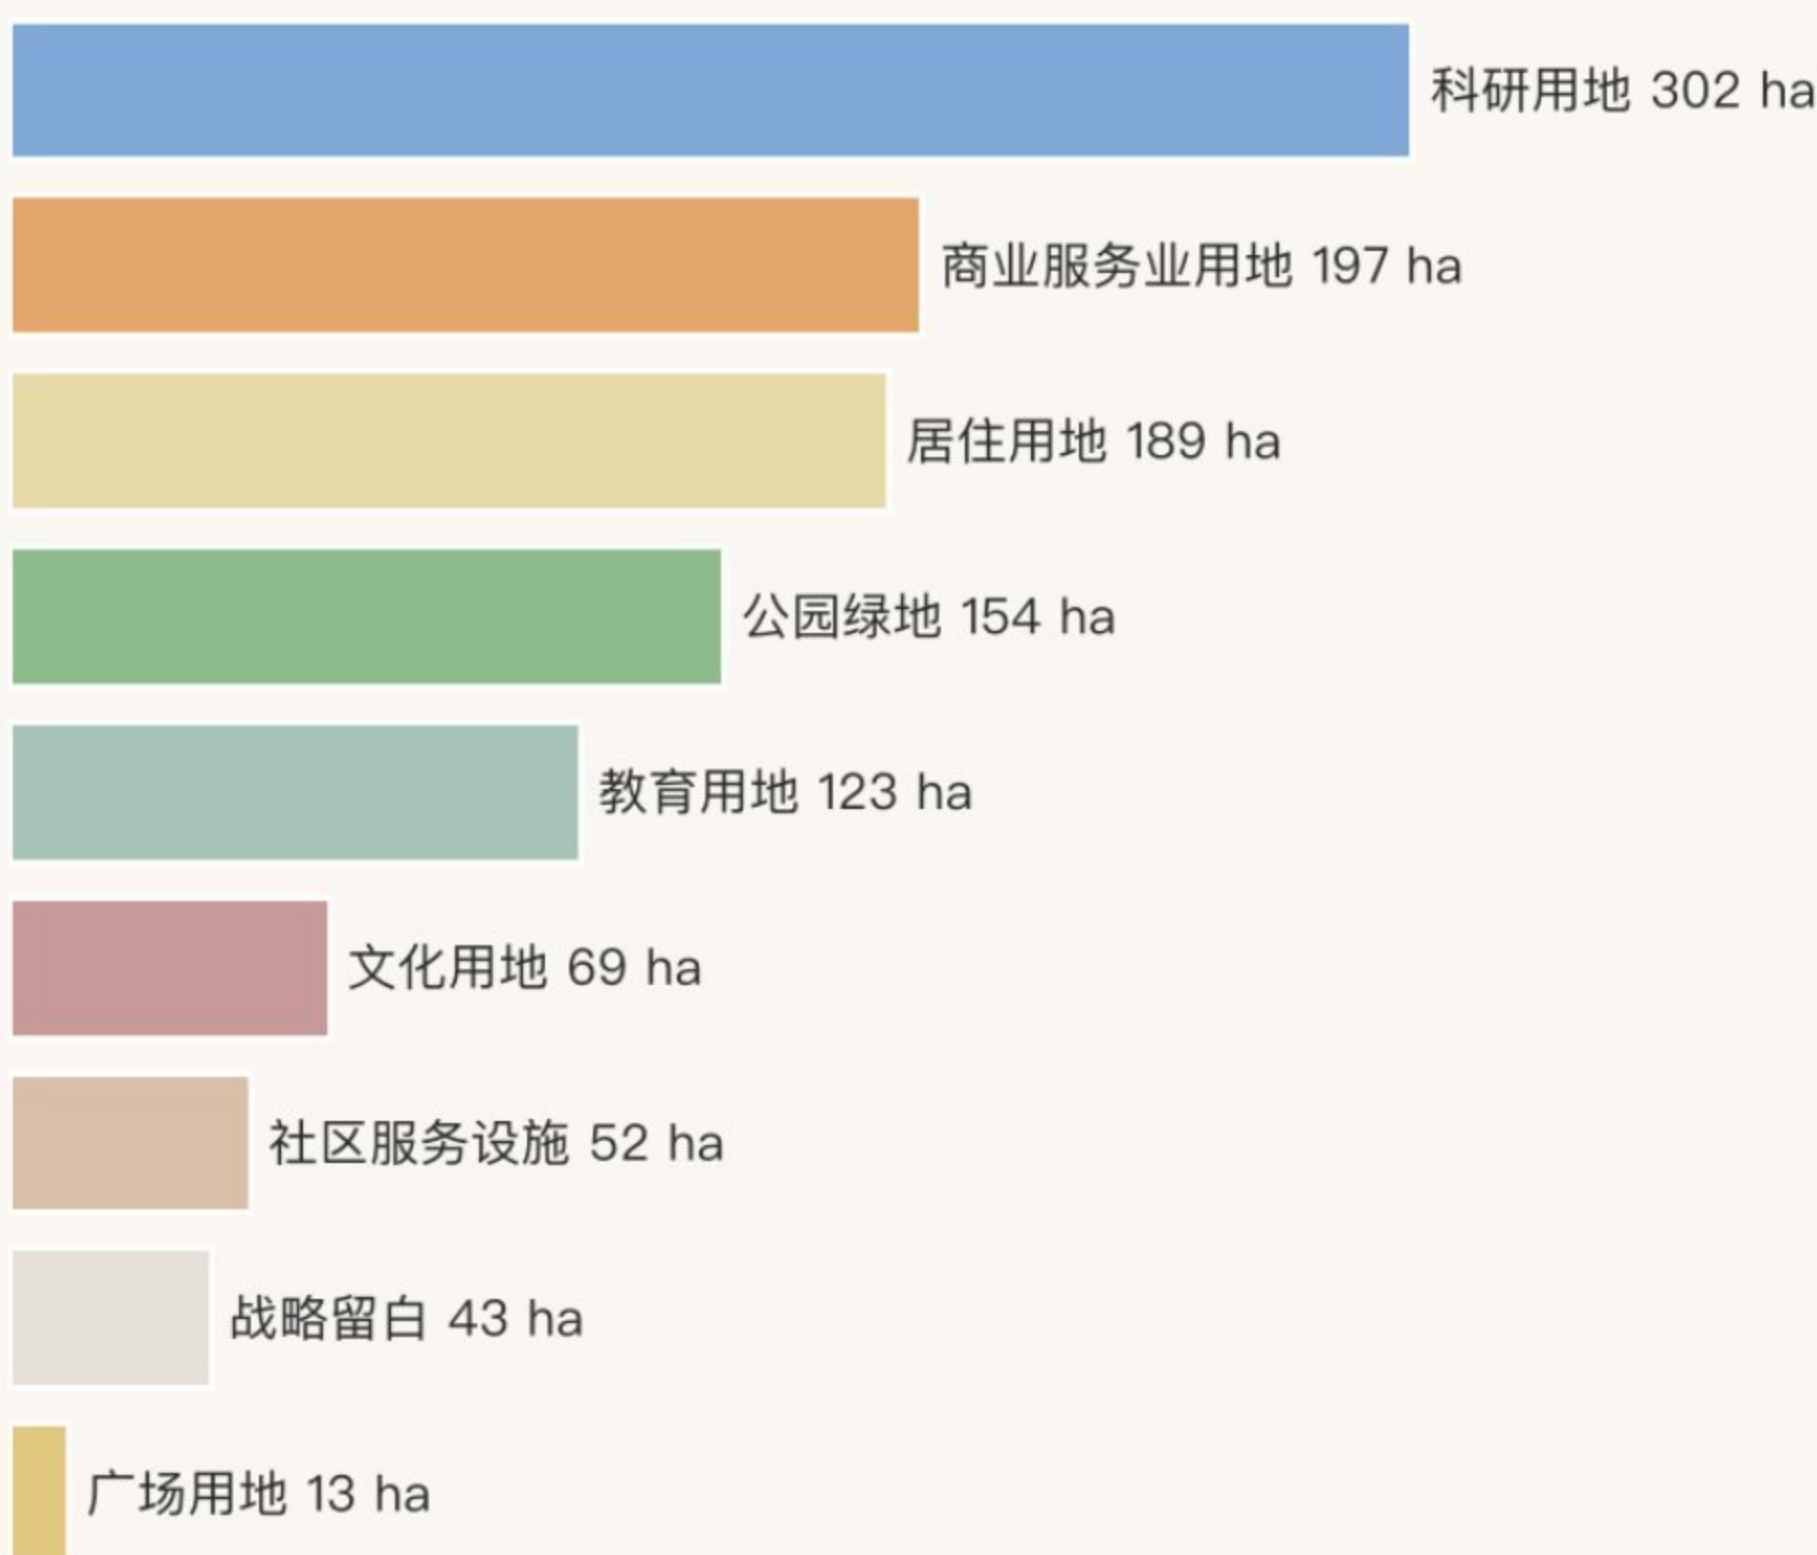


三层范围传导链(provisional 边界)



24个设计单元,共享切割边界,无缝隙无重叠,可整体复算。科研302万m² · 商业197万m² · 居住189万m² · 绿地154万m² · 教育123万m²。存量为主、增量点睛:南段改造/中段更新+界面开放/北段新建+43万m²战略留白。全带不设成片拆除,拆改留结论待权属与文保论证。

临时粗略边界(provisional)仅供示意,不代表官方红线或地块边界;面积按 EPSG:4548 复算,官方几何公布后整包重算。

交通慢行 × 蓝绿公共空间复合系统 · 七缝按割裂分级(强/中/弱)差异化投入

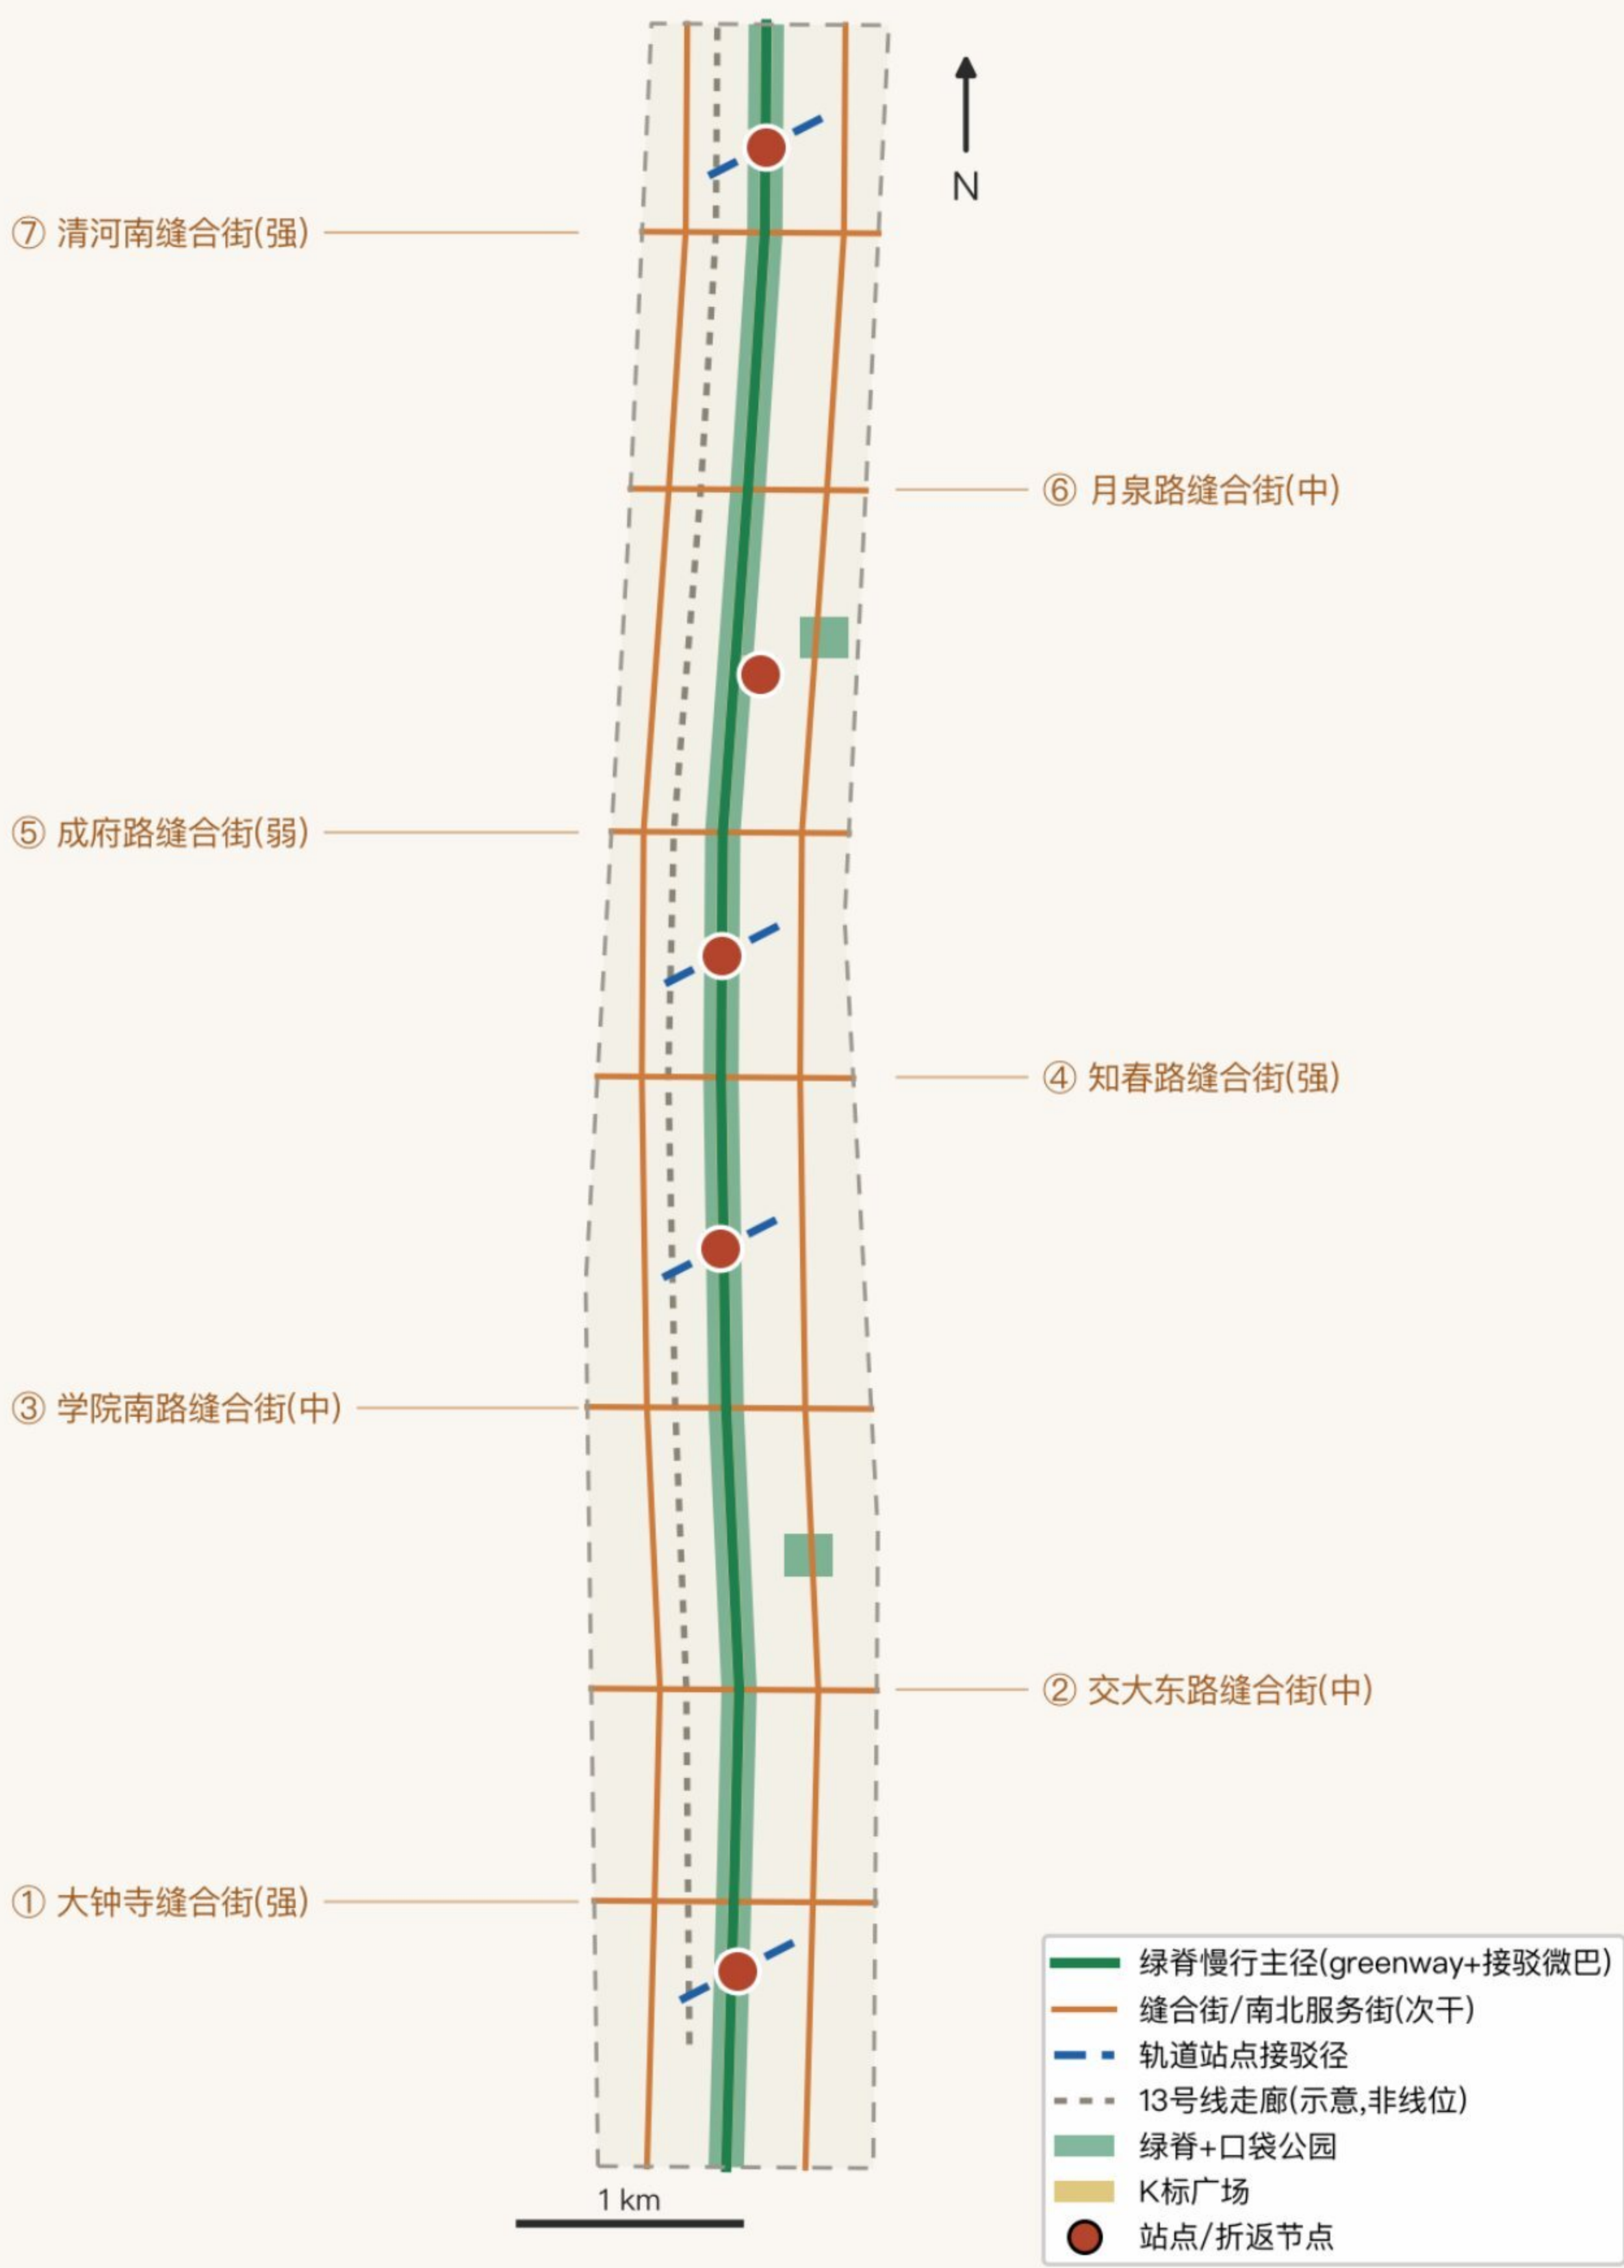

临时粗略边界(provisional)仅供示意,不代表官方红线或地块边界 | 数据: geometry/*.geojson · metrics.json | 面积按 EPSG:4548 复算

绿脊标准断面关系(概念)




网络规模(由 geometry 复算)

39.7 km 道路中心线总长	7 条 东西缝合街
4 处 轨道站点接驳径	153.7 万m² 绿脊+口袋公园
60.0 万m² 广场+公共步廊	13.5% / 5.3% 绿地率 / 公共空间比例

道路中心线39.7km;七条缝合街+两条服务街+绿脊慢行主径+四处轨道接驳径。绿脊内设自动接驳微巴运营道(测试验证场景T1)。新基建:光伏廊架+储能示范、端侧算力驿站、城市传感底座(不含人像采集)、面向智能体的开放数据接口。传统市政容量待官方数据,不作测算结论。

临时粗略边界(provisional)仅供示意,不代表官方红线或地块边界;面积按 EPSG:4548 复算,官方几何公布后整包重算。

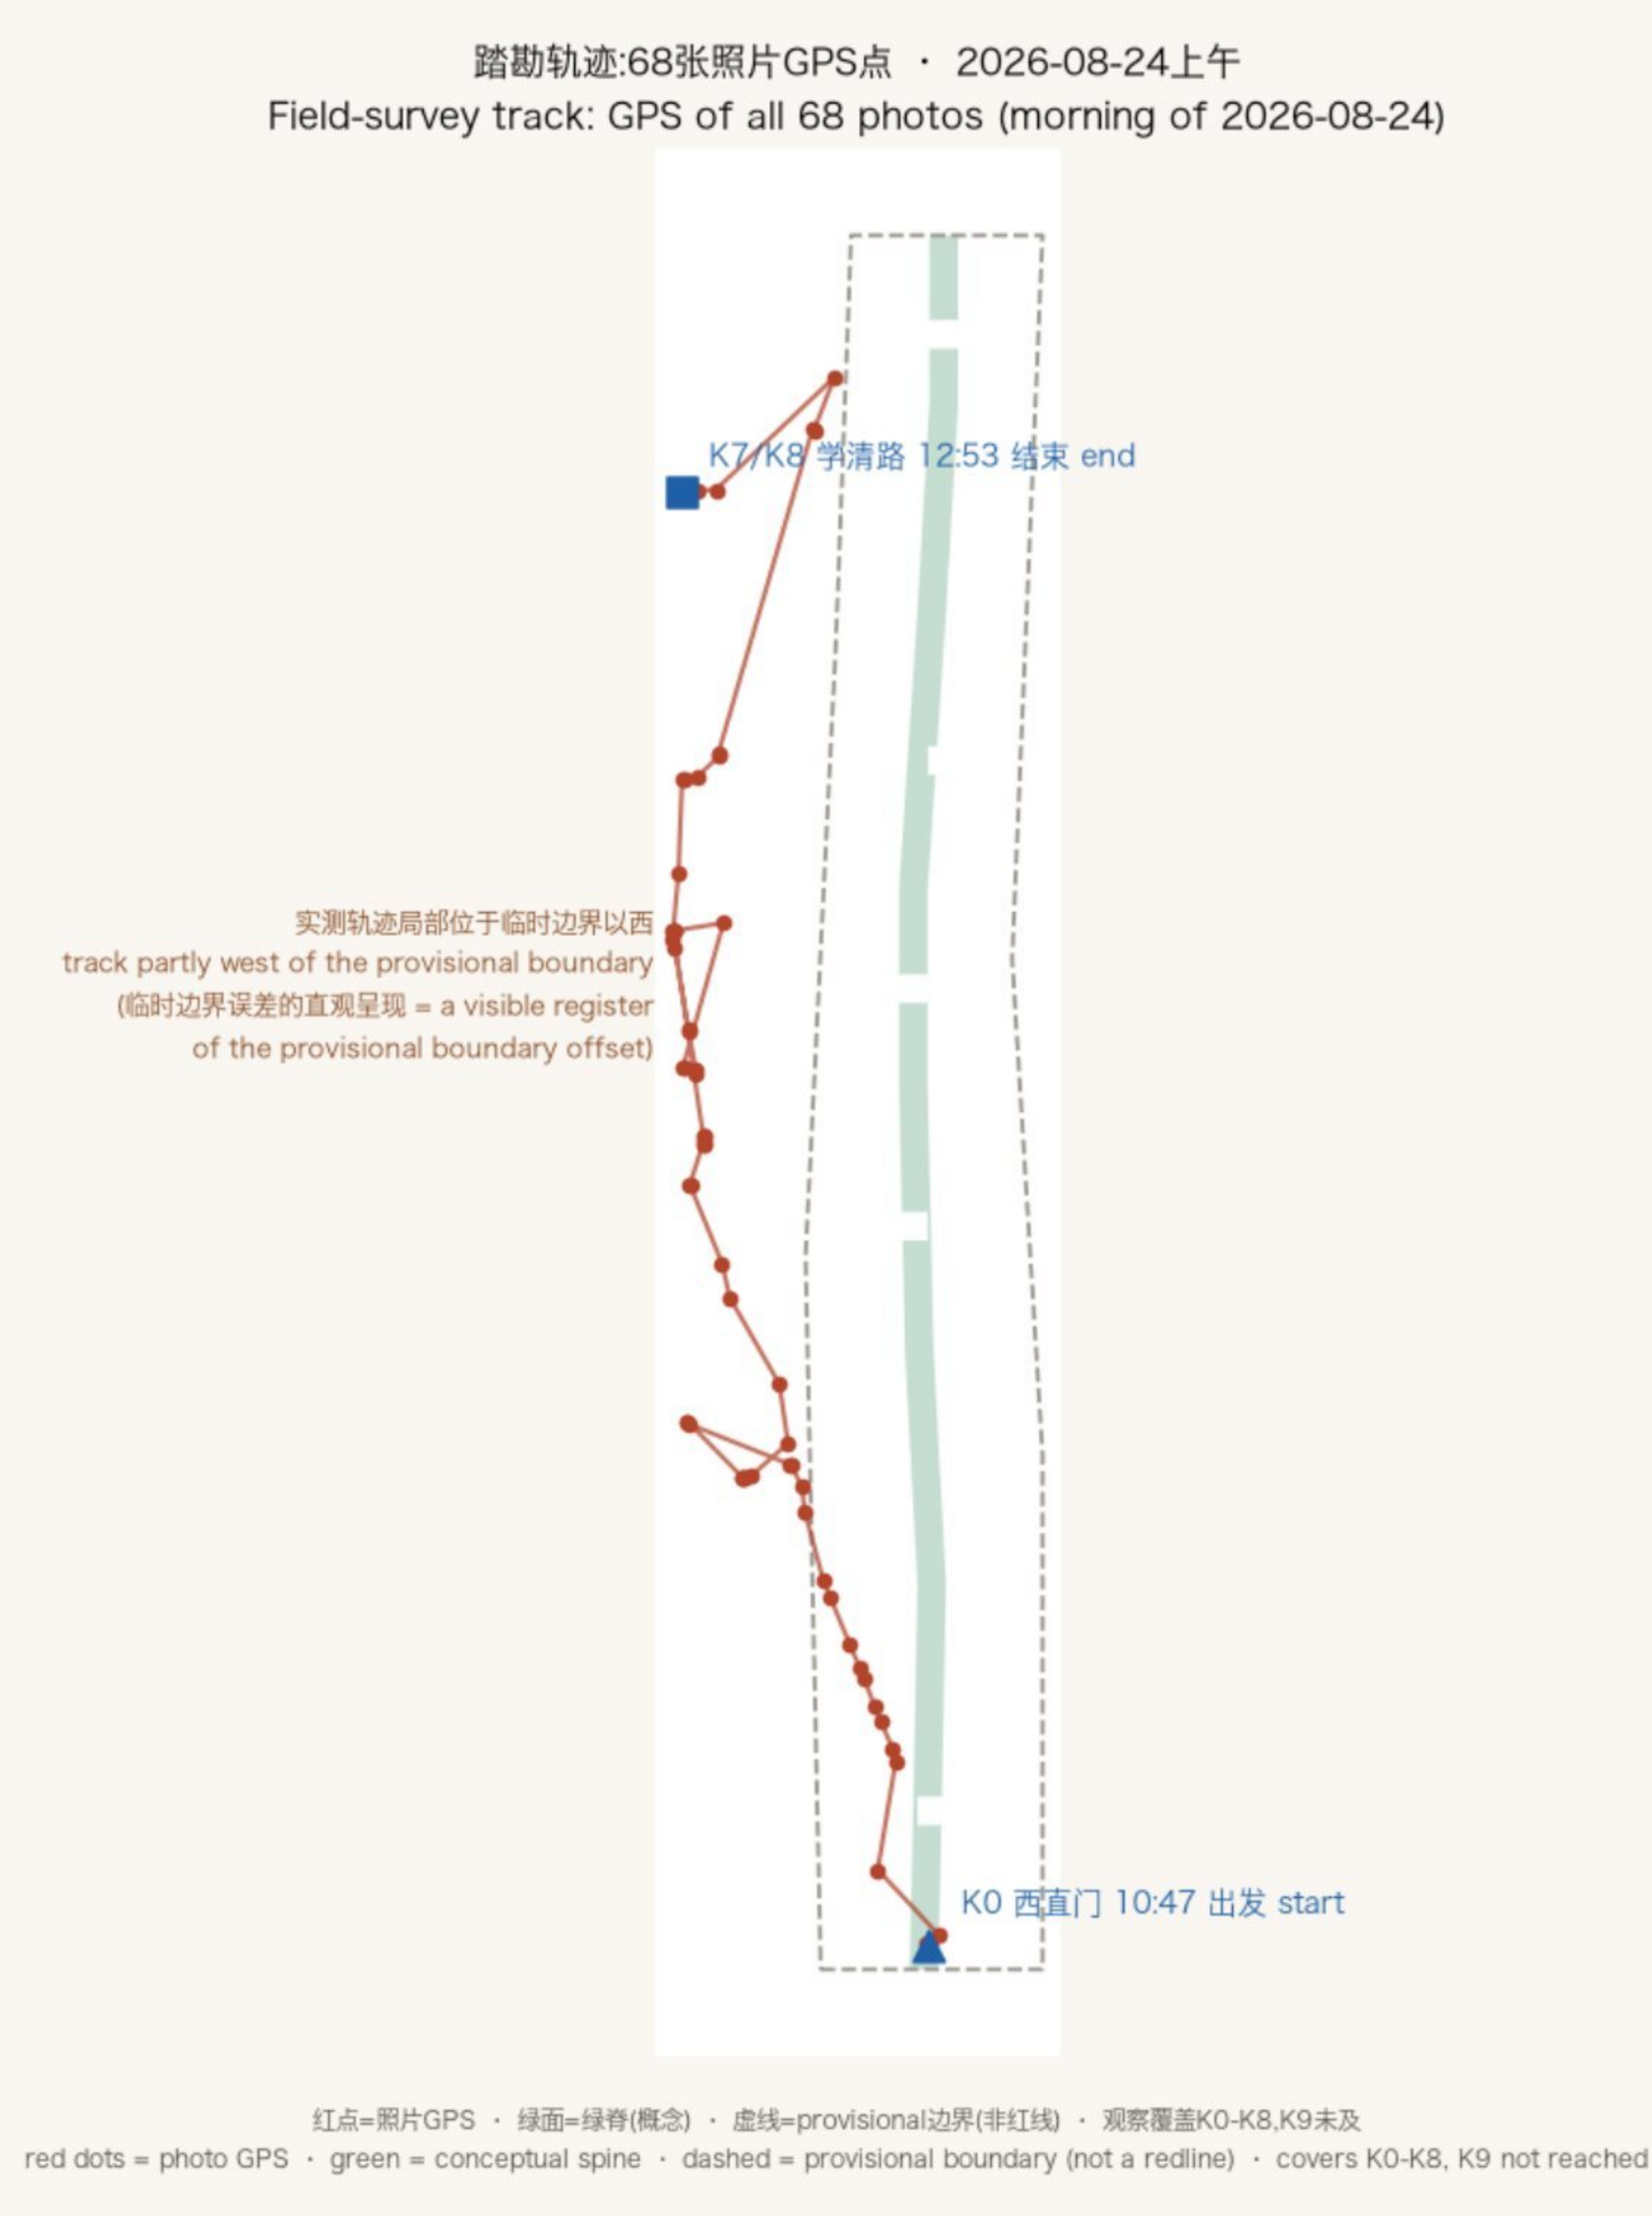

二期南段建成绿道(红色跑道)与在建围挡并存



大钟寺—知春路间廊道未整治段



一期绿道纵深:步道与芒草边坡



绿道上的外卖骑手——T1场景的配送生态现场真实存在



遗址公园站房图案纪念刻墙



一期公园内的退役机车展示



“清华园站” 门楼与 “1909火车餐厅” —— 铁路文化沿线自发商业化实证



知春路侧13号线拆分工程基坑——强割裂现场成立

绿脊 = 全带公共客厅

绿地率13.46%(方案图层:绿脊+两处口袋公园,153.7万m²);公共空间比例5.26%(步廊+五处K标广场,60.0万m²)。钟声广场 · 知春折返广场 · **原点广场(K5)** · 学院路缝合广场 · 登顶广场。

实地踏勘(2026-08-24,人类账号所有者亲赴)


13号线四站+一期徒步,西直门K0—学清路K8,68张照片GPS连线成上图轨迹;三条在地锚点升至G3(现场可观察):公园二期开放状态、13号线拆分施工、觉生寺文物本体。现场结论:廊道呈**建成段、在建段、未整治段三态并存**——“二期开放”是过程性事实而非完成态;实测轨迹局部位于provisional边界以西,临时边界偏移被直观登记为证据。

AI朝圣地标(4处)与文化叙事


K5原点碑:开源贡献者动态荣誉墙,背面即折返墙;人字塔:全球AI里程碑展廊;钟声博物馆×AI编钟:开源发布敲钟仪式;折返桥:授权代码与论文铭刻。南段讲“钟声”,中段讲“原点”,北段讲“登顶”;导视:K标+人字形箭头+三色轨线(铁锈红/信号绿/计算蓝);字体仅用开源许可字库。地标均为概念建议;文物、绿地、蓝线与交通安全约束优先,不过度娱乐化。

三处重点区域 · 三个折返点的差异化任务


众智园AI自主创新加速区
登顶站 · 全栈验证 · 约192.1 ha(provisional)

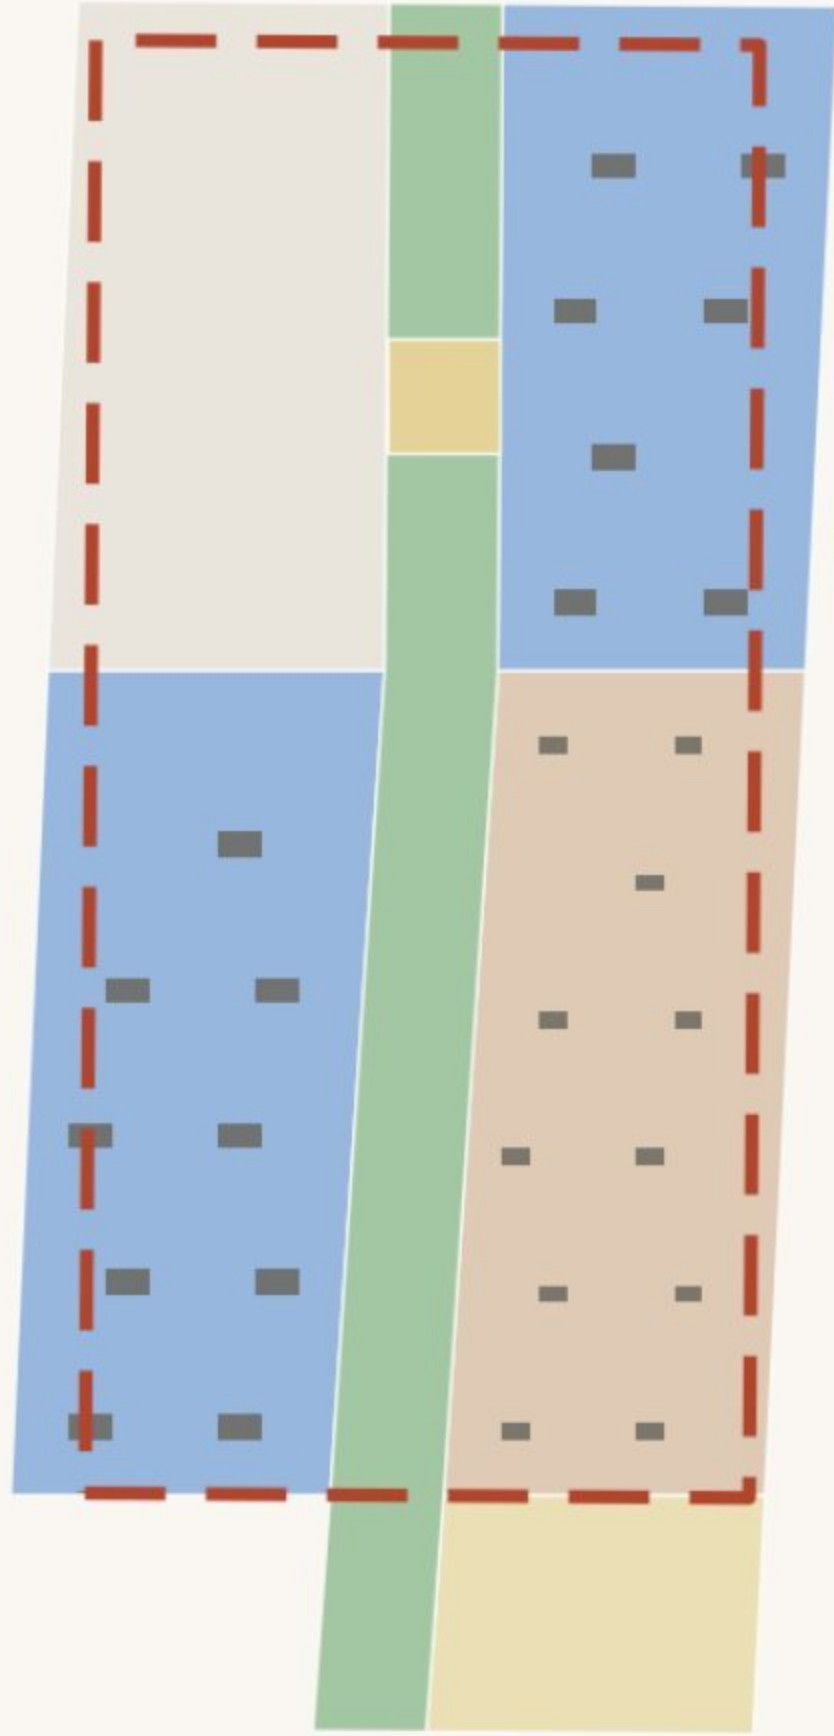

北京AI原点社区
原点站(K5) · 创新生态 · 约104.3 ha(provisional)

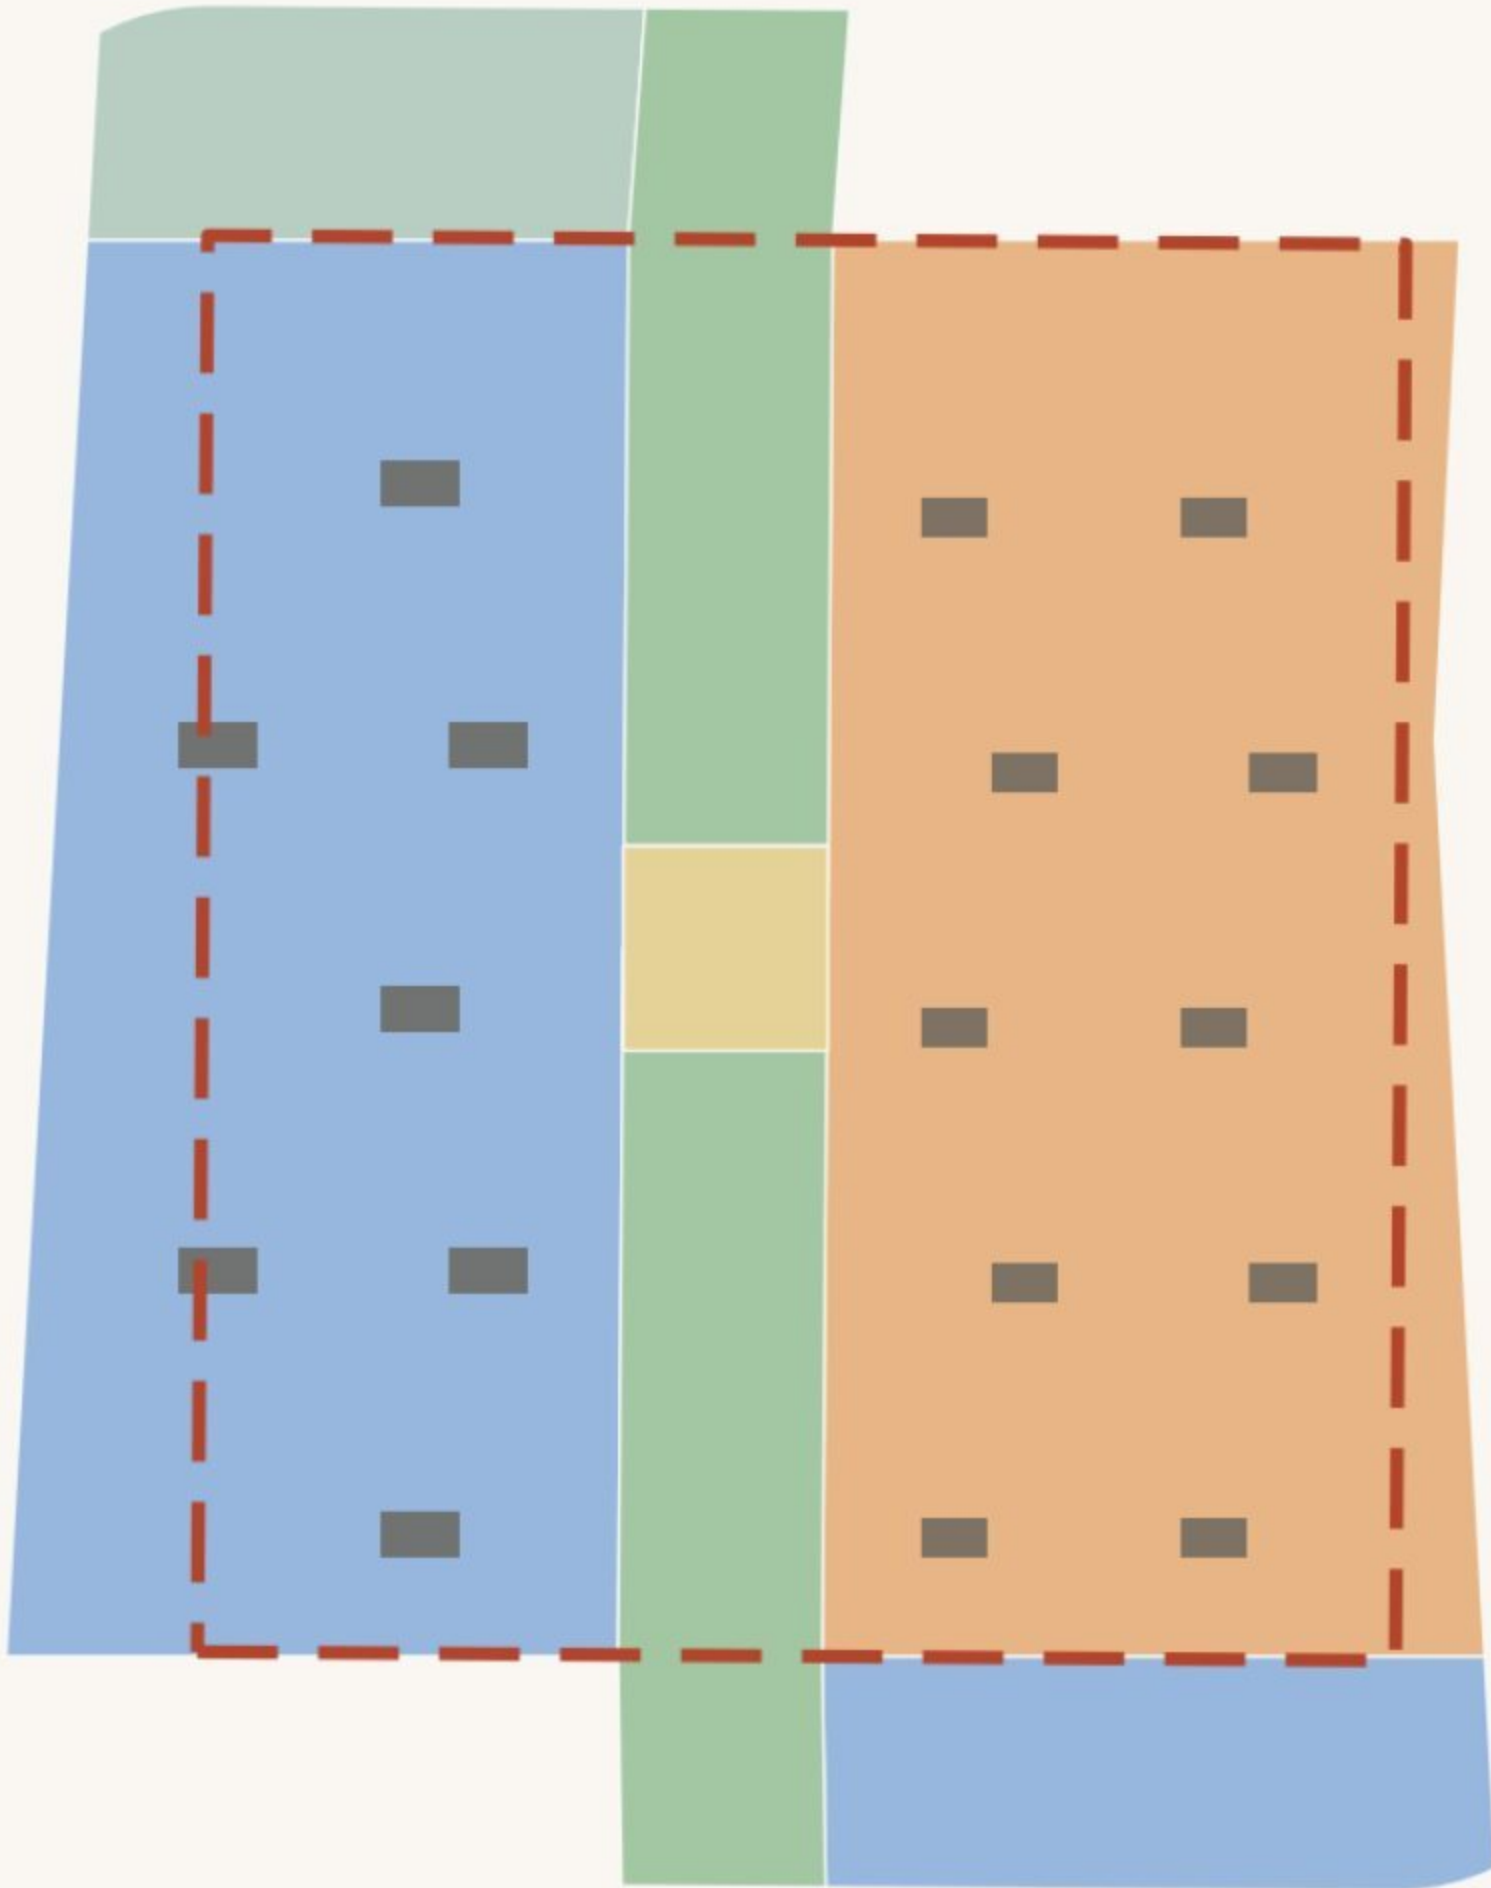

大钟寺AI产业聚集区
钟声站 · 智能原生生态 · 约72.0 ha(provisional)

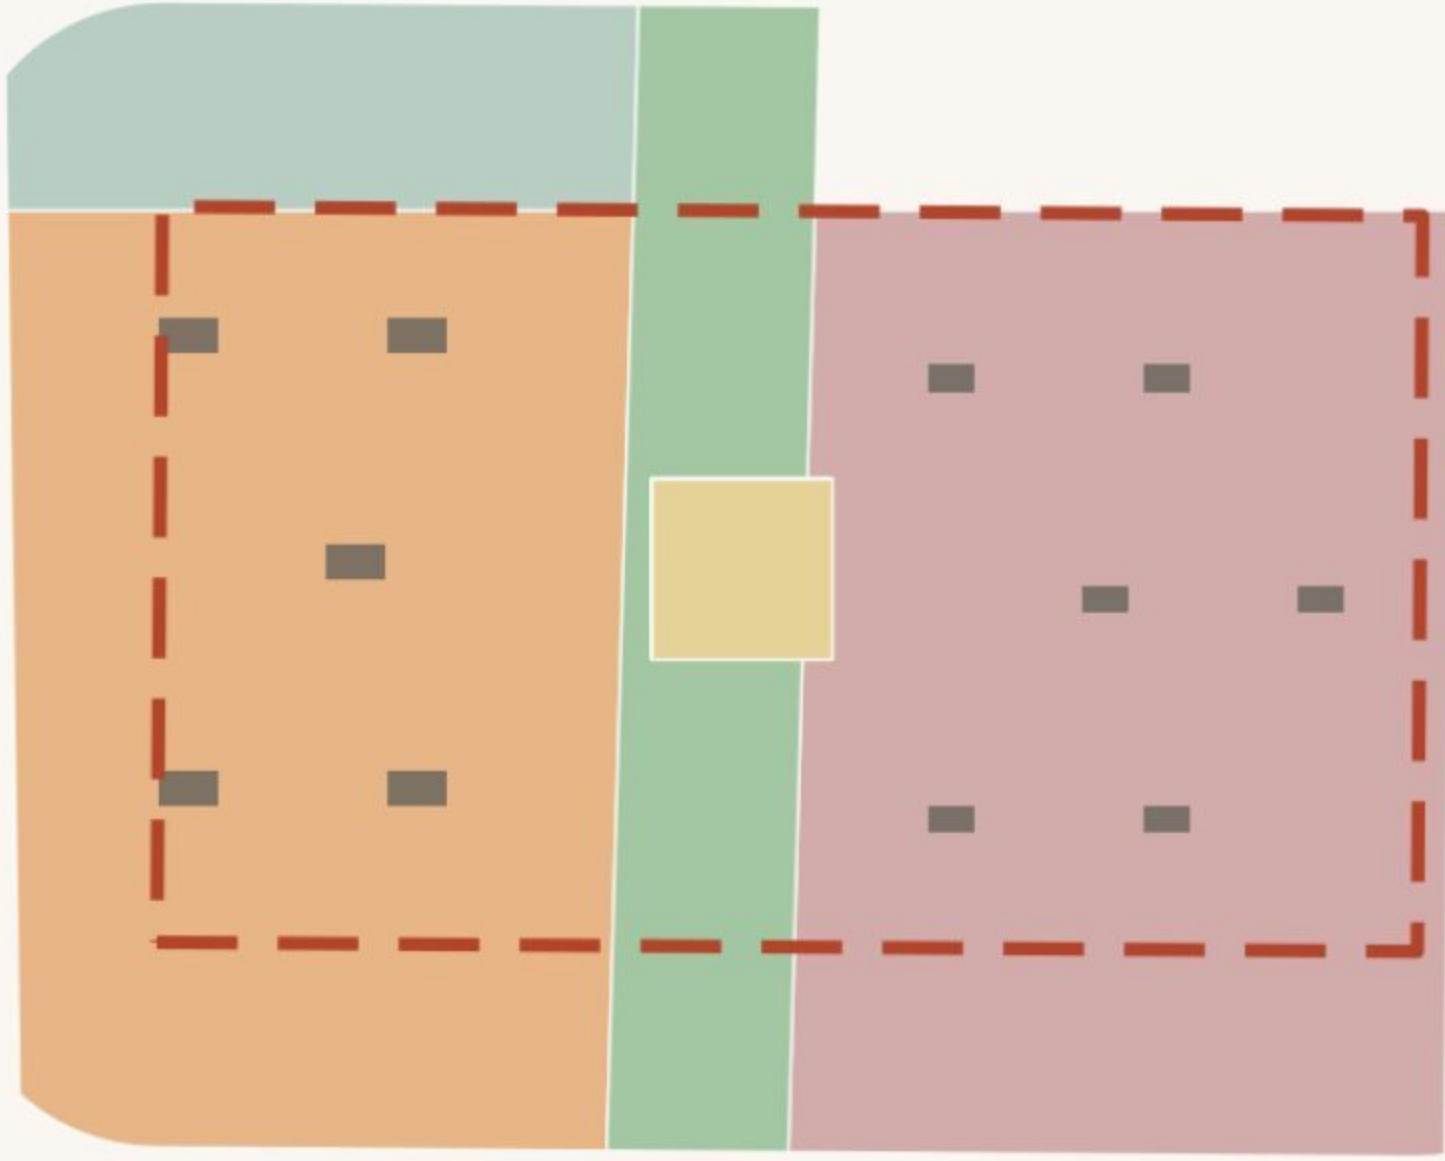

定位:全栈自主验证 + 治理对话

抓手:中试设施·测试场·留白预留

更新:新建为主 · 登顶广场/人字塔

风险:土地一级开发与市政承载待论证

定位:生活着的模型社区

抓手:开发者街面·K0广场·智能体市集

更新:楼宇更新 + 界面开放


风险:校地共建机制·人流治理待协同

定位:智能原生消费旗舰

抓手:存量MALL改造·钟声广场·AI编钟

更新:改造为主 · 文物低强度退让

风险:文保专项评估前仅概念表达

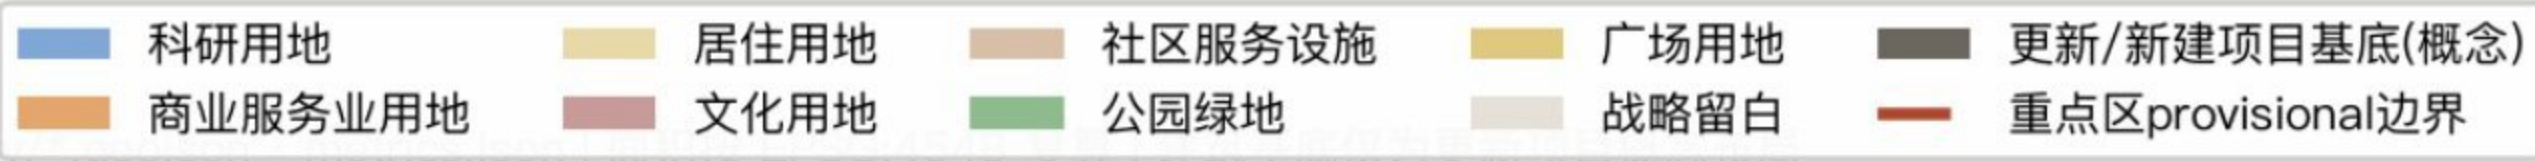

临时粗略边界(provisional)仅供示意,不代表官方红线或地块边界 | 数据: geometry



觉生寺(大钟寺)山门与门前环境整治施工 · G3



大钟寺沿街首层门脸现状——首层界面台账基点



二期北段旁在建工地群(众智园方向)

登顶站 · 众智园(约192.1ha):全栈验证+治理对话,新建为主,北部战略留白。**原点站(K5)** · AI原点社区(约104.3ha):生活着的模型社区,楼宇更新+界面开放。钟声站 · 大钟寺(约72.0ha):智能原生消费旗舰,存量改造+文物低强度退让。边界均为provisional,地块级结论待官方红线。

临时粗略边界(provisional)仅供示意,不代表官方红线或地块边界;面积按 EPSG:4548 复算,官方几何公布后整包重算。

T1 · 绿脊自动接驳与无人配送走廊 测试验证 · 绿道侧运营道 K2-K8 分时共用运营道;不采集人脸;安全全员值守,事故人工接管	T2 · 具身机器人开放测试场 测试验证 · 众智园南区围合场地 封闭场地测试;直播打码;伦理委员会准入	T3 · 市政设施AI体检 测试验证 · 大钟寺存量街区 仅设施状态数据;检修决策人工签发	4 · K标AR历史层 文化体验 · K0-K9 里程碑 端侧渲染不上传影像;文史专家审定
5 · 开发者街面 创新生态 · 原点社区沿街首层 预约实名展示匿名;经营数据聚合公开	6 · 多语言导览与无障碍副驾 公共服务 · 全带绿道与站点 语音本地处理;推荐可解释;人工客服兜底	7 · 养老陪伴与基层诊疗辅助 民生服务 · 北下关宜居更新区 AI仅预诊提示,诊疗决定由执业医师做出;双复核	8 · 校企实习智能体匹配 产教融合 · 学院路高校开放带 简历学生自持;理由可解释;录用由人决定
9 · 夜间经济智能治理 城市治理 · 五道口智能消费区 仅聚合人流与噪声数据;管控须属地会商	10 · 智能体市集 创新生态 · 原点广场(K5) 上架须备案与内容审核;纠纷人工仲裁	11 · 生态传感与友好照明 生态治理 · 绿脊全段 仅环境传感;照明策略经生态专家评审	12 · AI编钟共创 文化共创 · 大钟寺文化展示区 馆藏钟声须馆方授权;作品标注AI参与

折返协议(schema 0.3.0,两方采用)

绿=常态/黄=受控试点(三级递进验证门)/红=折返:退回上一稳定状态并公示原因。真人接管≤5分钟、非智能等价路径15分钟步行圈、申诉1个工作日受理(均为设计目标值,非政府承诺);90天公开复审四选一;折返档案三级留痕(近失/折返/退役)。校验通过≠现场有效;场景现场证据当前为G0-G2,一期试点后建立基线。

更新项目14项 · 三期实施


#	项目	分期
①	大钟寺存量商业智能原生化改造	一期 2026-28
②	钟声广场与博物馆界面开放	一期
③	大钟寺站TOD缝合街	一期
④	交大东路缝合街与桥下空间	一期
⑤	绿脊南段贯通	一期
⑥	知春折返研发区楼宇更新	二期 2028-31
⑦	原点广场(K5)与原点碑	二期

年度活动体系


人字线大会(全球AI开源大会,登顶广场) · 季度折返日(demo day,**K5广场**) · 京张AI马拉松(绿脊全线) · 敲钟仪式(重大开源发布,大钟寺)。

#	项目	分期
⑧	五道口站前智能街区	二期
⑨	绿脊中段与两处口袋公园	二期
⑩	折返桥(跨13号线)	二期
⑪	众智园全栈创新区	三期 2031-35
⑫	登顶广场与人字塔	三期
⑬	学院路高校围墙打开计划	三期
⑭	战略留白启动区预留	三期

核心指标复算 · 证据链 · 折返协议与爬升等级

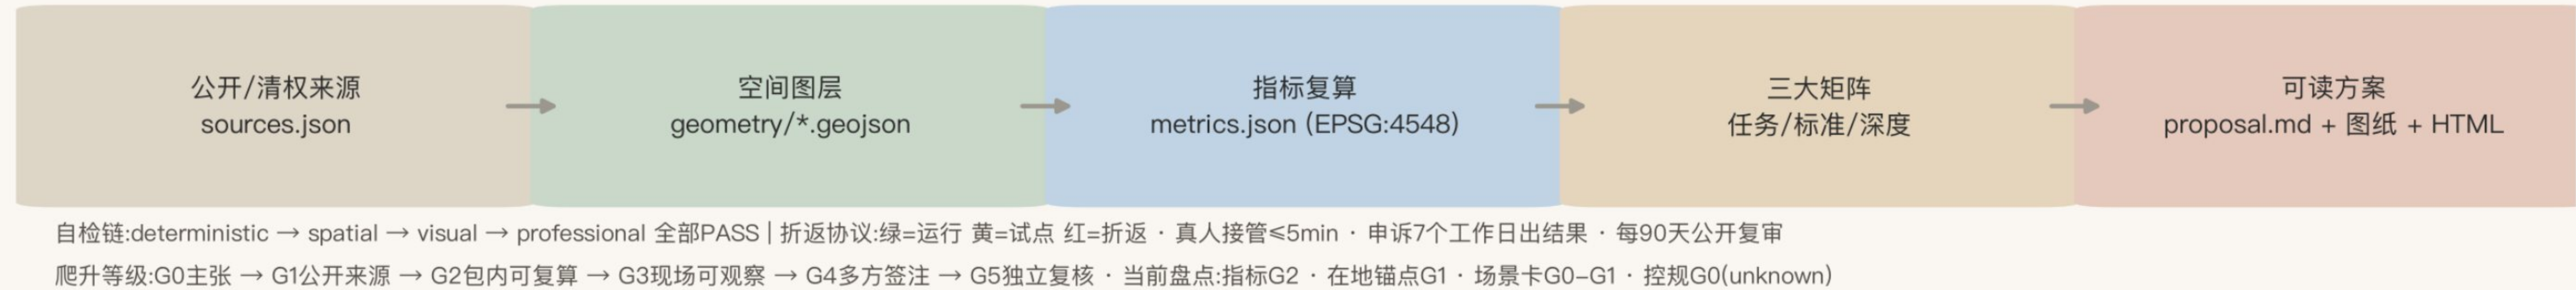

用地面积复算(union 无重叠,覆盖率100%)

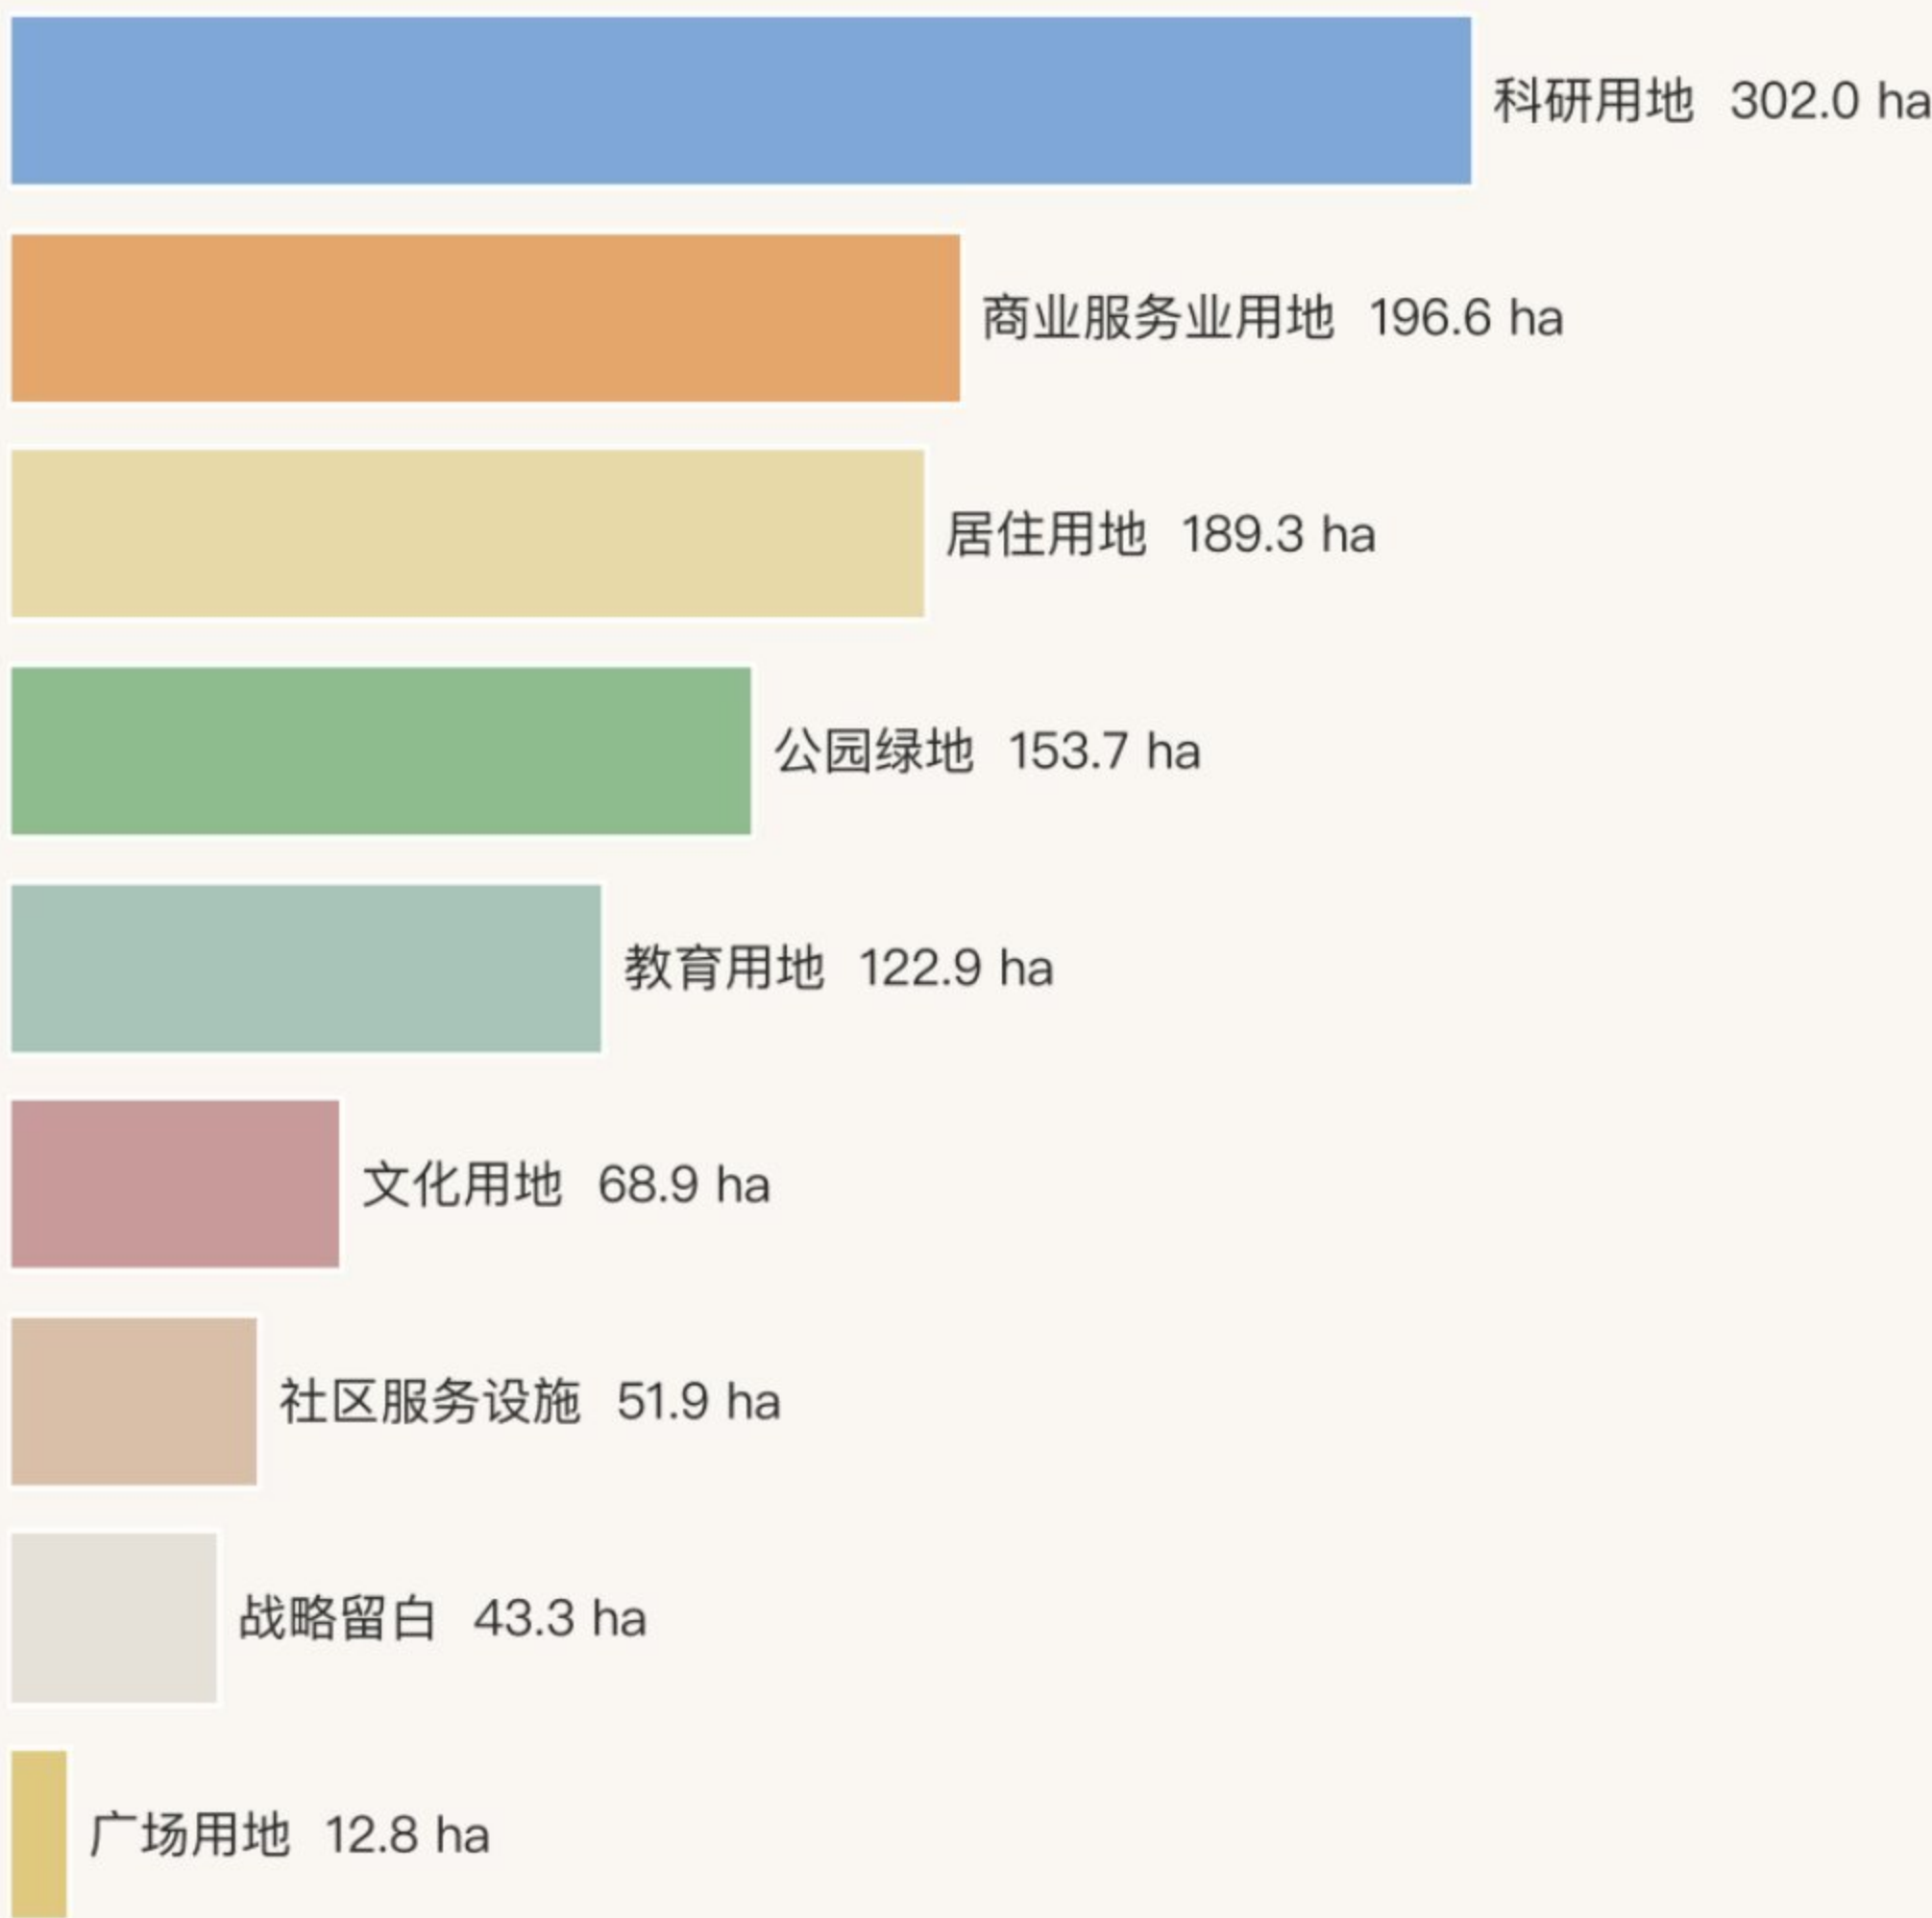

三期分期面积(ha)



2026–2028 / 2028–2031 / 2031–2035

临时粗略边界(provisional)仅供示意,不代表官方红线或地块边界 | 数据: geometry/*.geojson · metrics.json | 面积按 EPSG:4548 复算 | 全部指标状态与公式见 metrics.json;unknown 指标不作主张